


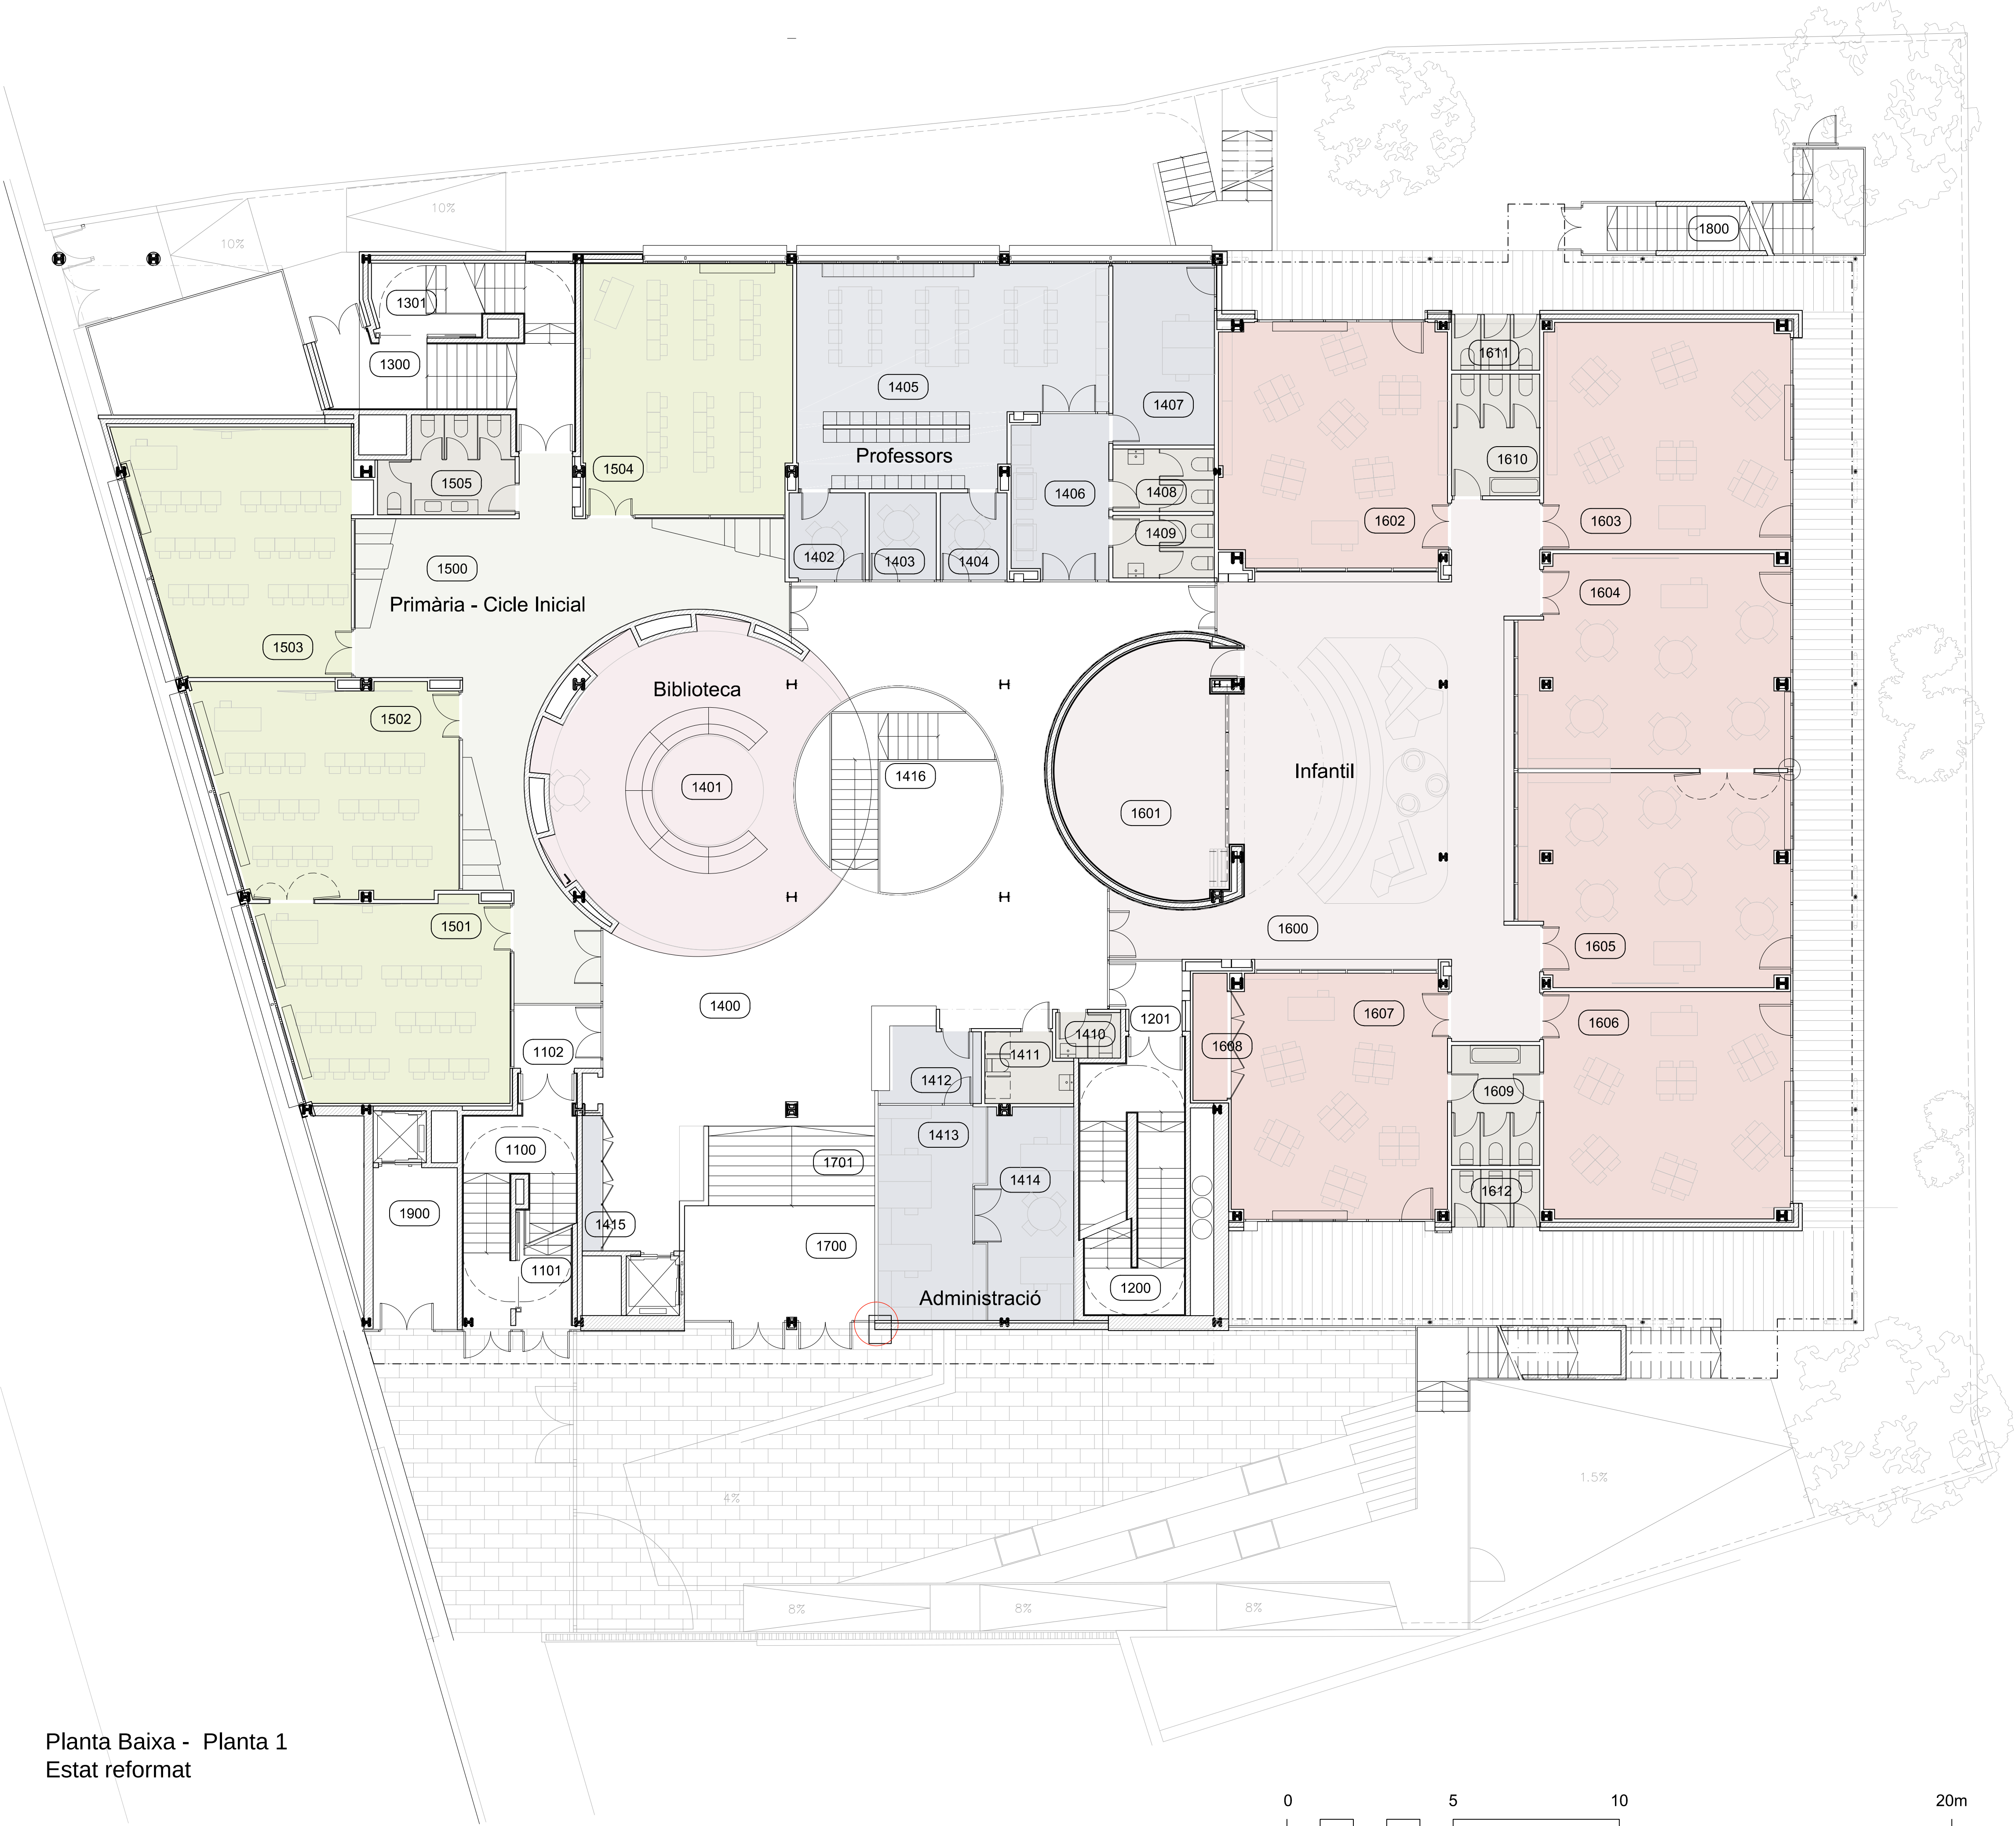

Planta Baixa - Planta 1
Estat reformat

RESUM ESTAT REFORMAT			
Planta	S.Construïda	Sup Útil	S Exterior
Semi Soterrani	1647.9 m²	1457.2 m²	0.0 m²
Planta Baixa - Planta 1	1604.2 m²	1318.5 m²	876.1 m²
Planta 2	886.4 m²	770.5 m²	757.9 m²
Planta 3	857.2 m²	770.2 m²	0.0 m²
Planta 4	811.3 m²	708.1 m²	96.8 m²
Planta Coberta	34.5 m²	13.2 m²	721.3 m²
TOTAL	5841.5 m²	5037.7 m²	2452.1 m²

SUP ÚTIL PLANTA BAIXA			
Num	Espai		Sup Útil
1100	Escala - A	Circulació	17.3 m²
1101	Escala - A1	Circulació	4.8 m²
1102	Vestíbul	Circulació	5.0 m²
1200	Escala - B	Circulació	23.1 m²
1201	Vestíbul	Circulació	4.4 m²
1300	Escala - C	Circulació	23.4 m²
1301	Escala - C1	Circulació	6.8 m²
1400	Espai - Comú	Circulació	132.2 m²
1401	Biblioteca	Biblioteca	69.4 m²
1402	Sala - Professors	Professors	6.0 m²
1403	Sala - Professors	Professors	5.3 m²
1404	Sala - Professors	Professors	5.3 m²
1405	Sala - Professors	Professors	55.8 m²
1406	Sala - Reprografia	Professors	14.1 m²
1407	Sala - AFA	Professors	16.7 m²
1408	Lavabos - Professors	Professors	5.7 m²
1409	Lavabos - Professors	Professors	5.7 m²
1410	Lavabos	Banys - Vestidors	2.7 m²
1411	Lavabo adaptat	Banys - Vestidors	5.2 m²
1412	Secretaria	Administració	6.1 m²
1413	Administració	Administració	20.3 m²
1414	Despatx	Administració	17.5 m²
1415	Armari elèctric	Espais - Tècnic	2.3 m²
1416	Escala - F1	Circulació	10.1 m²
1500	Espai - Comú	Primària - Cicle Inicial	76.6 m²
1501	Aula	Primària - Cicle Inicial	41.9 m²
1502	Aula	Primària - Cicle Inicial	46.4 m²
1503	Aula	Primària - Cicle Inicial	46.6 m²
1504	Aula	Primària - Cicle Inicial	47.2 m²
1505	Lavabos	Primària - Cicle Inicial	10.9 m²
1600	Espai - Comú	Infantil	120.1 m²
1601	Sala - Polivalent	Infantil	34.3 m²
1602	Aula	Infantil	50.0 m²
1603	Aula	Infantil	50.6 m²
1604	Aula	Infantil	50.9 m²
1605	Aula	Infantil	50.9 m²
1606	Aula	Infantil	50.5 m²
1607	Aula	Infantil	47.6 m²
1608	Armari Aula	Infantil	3.9 m²
1609	Lavabos	Infantil	9.6 m²
1610	Lavabos	Infantil	9.7 m²
1611	Lavabos	Pati - Infantil	4.1 m²
1612	Lavabos	Pati - Infantil	4.5 m²
1700	Vestíbul accés	Circulació	20.8 m²
1701	Escala accés	Circulació	12.0 m²
1800	Escala - E1	Circulació	8.0 m²
1900	Zona - Càrrega i descàrrega	Manteniment	12.0 m²
0			

SUP EXTERIOR PLANTA BAIXA		
Espai		Sup Útil
Porxo	Pati - Infantil	147.8 m²
Pati - Exterior	Pati - Infantil	325.3 m²
Zona exterior accés		238.0 m²
Zona exterior carrer	Circulació	47.8 m²
Zona exterior lateral	Circulació	112.3 m²
Porxo	Circulació	4.3 m²
TOTAL		875.5 m²