


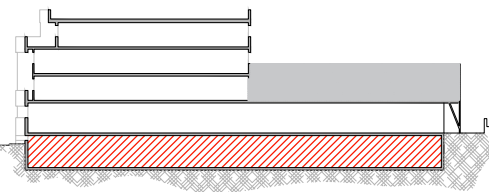


RESUM ESTAT REFORMAT			
Planta	S.Construïda	Sup Útil	S Exterior
Semi Soterrani	1647.9 m²	1457.2 m²	0.0 m²
Planta Baixa - Planta 1	1604.2 m²	1318.5 m²	876.1 m²
Planta 2	886.4 m²	770.5 m²	757.9 m²
Planta 3	857.2 m²	770.2 m²	0.0 m²
Planta 4	811.3 m²	708.1 m²	96.8 m²
Planta Coberta	34.5 m²	13.2 m²	721.3 m²
TOTAL	5841.5 m²	5037.7 m²	2452.1 m²

SUP ÚTIL PLANTA SEMI SOTERRANI			
Num	Espai		Sup Útil
S100	Escala - A1	Circulació	17.9 m²
S101	Vestíbul	Circulació	4.0 m²
S105	Magatzem	Manteniment	23.2 m²
S200	Escala - B1	Circulació	10.3 m²
S201	Escala - B	Circulació	3.8 m²
S300	Escala - C1	Circulació	11.4 m²
S301	Vestíbul	Circulació	7.8 m²
S302	Vestíbul	Circulació	5.4 m²
S303	Magatzem	Manteniment	23.1 m²
S500	Passadís	Circulació	45.7 m²
S501	Lavabos	Banyes - Vestídors	7.6 m²
S502	Lavabo adaptat	Banyes - Vestídors	5.4 m²
S503	Lavabos	Banyes - Vestídors	7.6 m²
S504	Espai Tècnic	Espais - Tècnic	8.4 m²
S505	Taller - Manteniment	Manteniment	18.1 m²
S506	Vestuari - Nens	Banyes - Vestídors	21.3 m²
S507	Vestuari - Nens	Banyes - Vestídors	21.3 m²
S508	Lavabo adaptat	Banyes - Vestídors	5.5 m²
S509	Espai Tècnic	Espais - Tècnic	4.7 m²
S600	Menjador - Nens	Menjador	214.1 m²
S601	Aula - Visual Plàstica	Plàstica	81.5 m²
S602	Taller - Tecnologia	Tecnologia	104.6 m²
S603	Aula - Música	Música	61.9 m²
S604	Vestíbul	Música	3.6 m²
S605	Escala - F1	Circulació	4.1 m²
S606	Aula - Música	Música	3.7 m²
S607	Aula - Música	Música	3.3 m²
S608	Aula - Música	Música	3.3 m²
S704	Aula - Auxiliar	Cuina	13.2 m²
S705	Cuina	Cuina	44.8 m²
S705	Vestuari - Treballadors	Cuina	5.4 m²
S705	Magatzem	Cuina	8.6 m²
S705	Zona - Preparacions fredes	Cuina	9.1 m²
S705	Magatzem	Cuina	10.1 m²
S705	Lavabos	Cuina	2.2 m²
S705	Passadís	Cuina	10.7 m²
S800	Gimnàs	Poliesportiu	167.2 m²
S801	Càmara envà mòbil	Poliesportiu	3.7 m²
S802	Magatzem	Poliesportiu	17.3 m²
S803	Magatzem	Circulació	26.4 m²
S804	Passadís	Circulació	13.4 m²
S805	Magatzem	Manteniment	8.2 m²
S806	Passadís	Circulació	21.3 m²
S807	Espai Tècnic	Espais - Tècnic	73.4 m²
S808	Espai Tècnic	Espais - Tècnic	16.3 m²
S900	Auditori	Auditori	116.8 m²
S901	Vestíbul	Auditori	4.3 m²
S902	Vestíbul	Auditori	5.5 m²
S903	Escenari lateral	Auditori	23.5 m²
S904	Escenari	Auditori	39.8 m²
S905	Escenari lateral	Auditori	12.2 m²
S906	Escala - E1	Circulació	6.3 m²
S907	Passadís	Auditori	8.5 m²
S908	Control	Auditori	8.3 m²

TOTAL



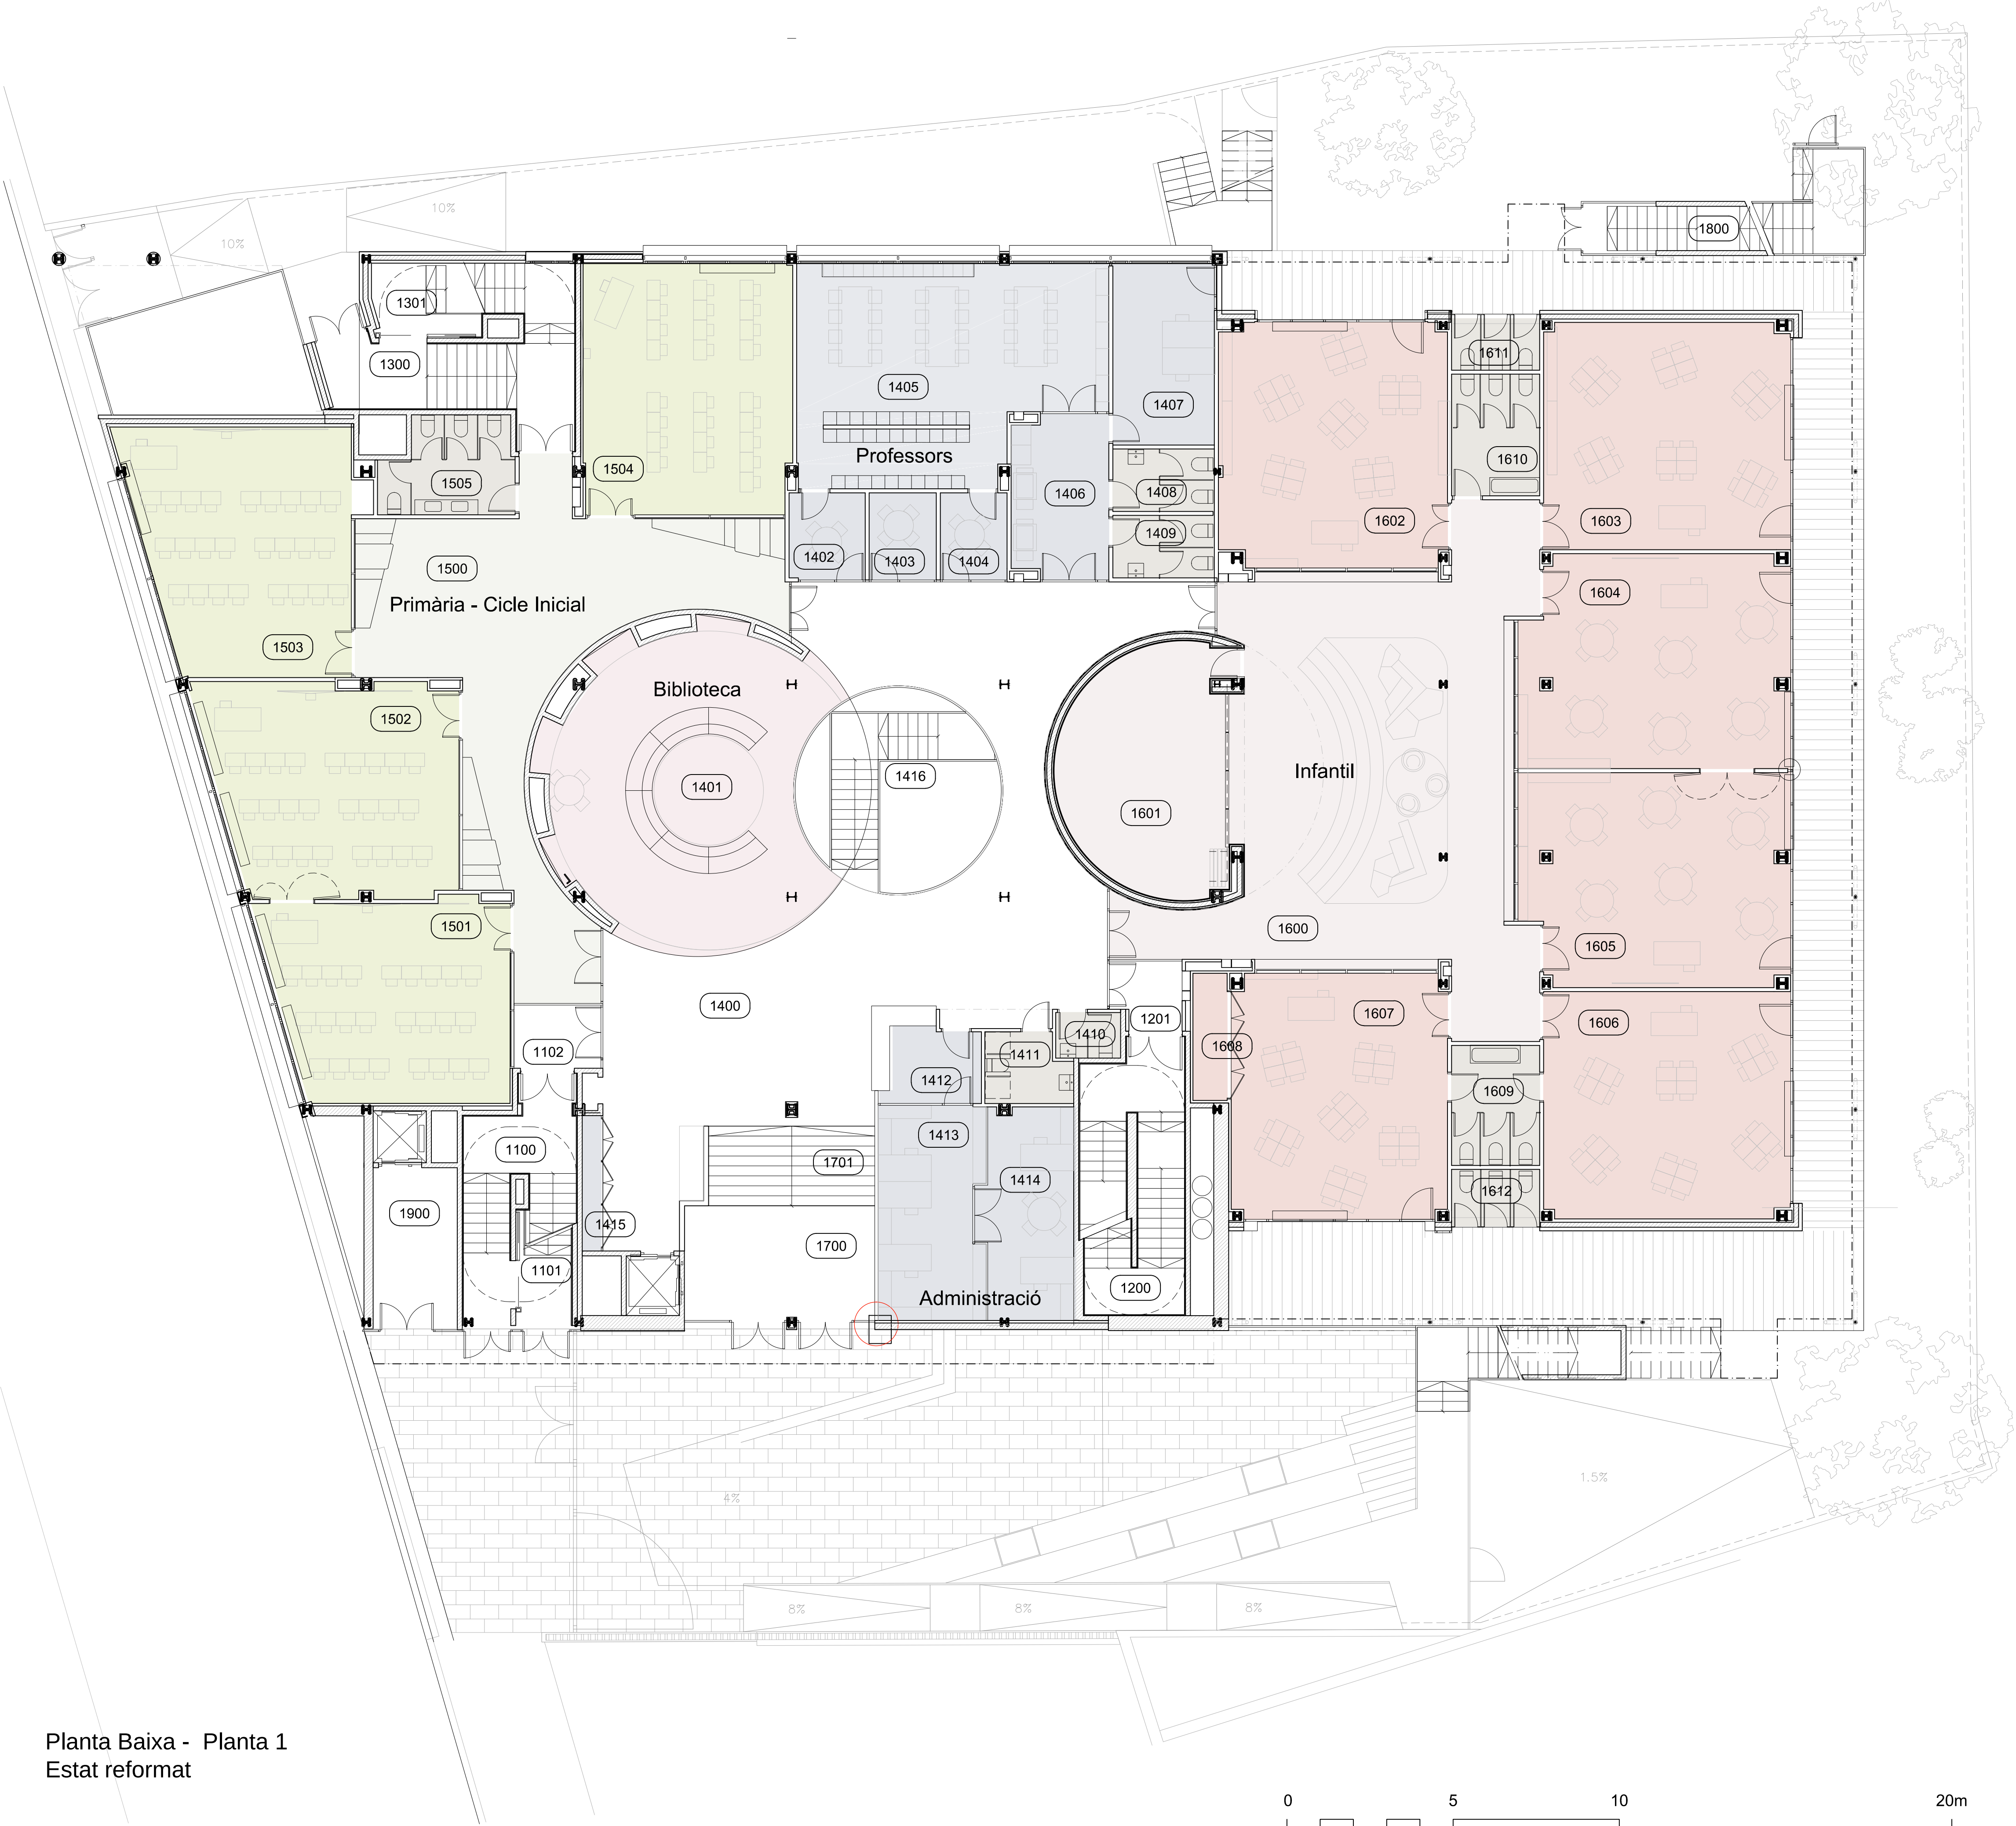


Planta Baixa - Planta 1
Estat reformat

RESUM ESTAT REFORMAT			
Planta	S.Construïda	Sup Útil	S Exterior
Semi Soterrani	1647.9 m²	1457.2 m²	0.0 m²
Planta Baixa - Planta 1	1604.2 m²	1318.5 m²	876.1 m²
Planta 2	886.4 m²	770.5 m²	757.9 m²
Planta 3	857.2 m²	770.2 m²	0.0 m²
Planta 4	811.3 m²	708.1 m²	96.8 m²
Planta Coberta	34.5 m²	13.2 m²	721.3 m²
TOTAL	5841.5 m²	5037.7 m²	2452.1 m²

SUP ÚTIL PLANTA BAIXA			
Num	Espai		Sup Útil
1100	Escala - A	Circulació	17.3 m²
1101	Escala - A1	Circulació	4.8 m²
1102	Vestíbul	Circulació	5.0 m²
1200	Escala - B	Circulació	23.1 m²
1201	Vestíbul	Circulació	4.4 m²
1300	Escala - C	Circulació	23.4 m²
1301	Escala - C1	Circulació	6.8 m²
1400	Espai - Comú	Circulació	132.2 m²
1401	Biblioteca	Biblioteca	69.4 m²
1402	Sala - Professors	Professors	6.0 m²
1403	Sala - Professors	Professors	5.3 m²
1404	Sala - Professors	Professors	5.3 m²
1405	Sala - Professors	Professors	55.8 m²
1406	Sala - Reprografia	Professors	14.1 m²
1407	Sala - AFA	Professors	16.7 m²
1408	Lavabos - Professors	Professors	5.7 m²
1409	Lavabos - Professors	Professors	5.7 m²
1410	Lavabos	Banys - Vestidors	2.7 m²
1411	Lavabo adaptat	Banys - Vestidors	5.2 m²
1412	Secretaria	Administració	6.1 m²
1413	Administració	Administració	20.3 m²
1414	Despatx	Administració	17.5 m²
1415	Armari elèctric	Espais - Tècnic	2.3 m²
1416	Escala - F1	Circulació	10.1 m²
1500	Espai - Comú	Primària - Cicle Inicial	76.6 m²
1501	Aula	Primària - Cicle Inicial	41.9 m²
1502	Aula	Primària - Cicle Inicial	46.4 m²
1503	Aula	Primària - Cicle Inicial	46.6 m²
1504	Aula	Primària - Cicle Inicial	47.2 m²
1505	Lavabos	Primària - Cicle Inicial	10.9 m²
1600	Espai - Comú	Infantil	120.1 m²
1601	Sala - Polivalent	Infantil	34.3 m²
1602	Aula	Infantil	50.0 m²
1603	Aula	Infantil	50.6 m²
1604	Aula	Infantil	50.9 m²
1605	Aula	Infantil	50.9 m²
1606	Aula	Infantil	50.5 m²
1607	Aula	Infantil	47.6 m²
1608	Armari Aula	Infantil	3.9 m²
1609	Lavabos	Infantil	9.6 m²
1610	Lavabos	Infantil	9.7 m²
1611	Lavabos	Pati - Infantil	4.1 m²
1612	Lavabos	Pati - Infantil	4.5 m²
1700	Vestíbul accés	Circulació	20.8 m²
1701	Escala accés	Circulació	12.0 m²
1800	Escala - E1	Circulació	8.0 m²
1900	Zona - Càrrega i descàrrega	Manteniment	12.0 m²
0			

SUP EXTERIOR PLANTA BAIXA		
Espai		Sup Útil
Porxo	Pati - Infantil	147.8 m²
Pati - Exterior	Pati - Infantil	325.3 m²
Zona exterior accés		238.0 m²
Zona exterior carrer	Circulació	47.8 m²
Zona exterior lateral	Circulació	112.3 m²
Porxo	Circulació	4.3 m²
TOTAL		875.5 m²

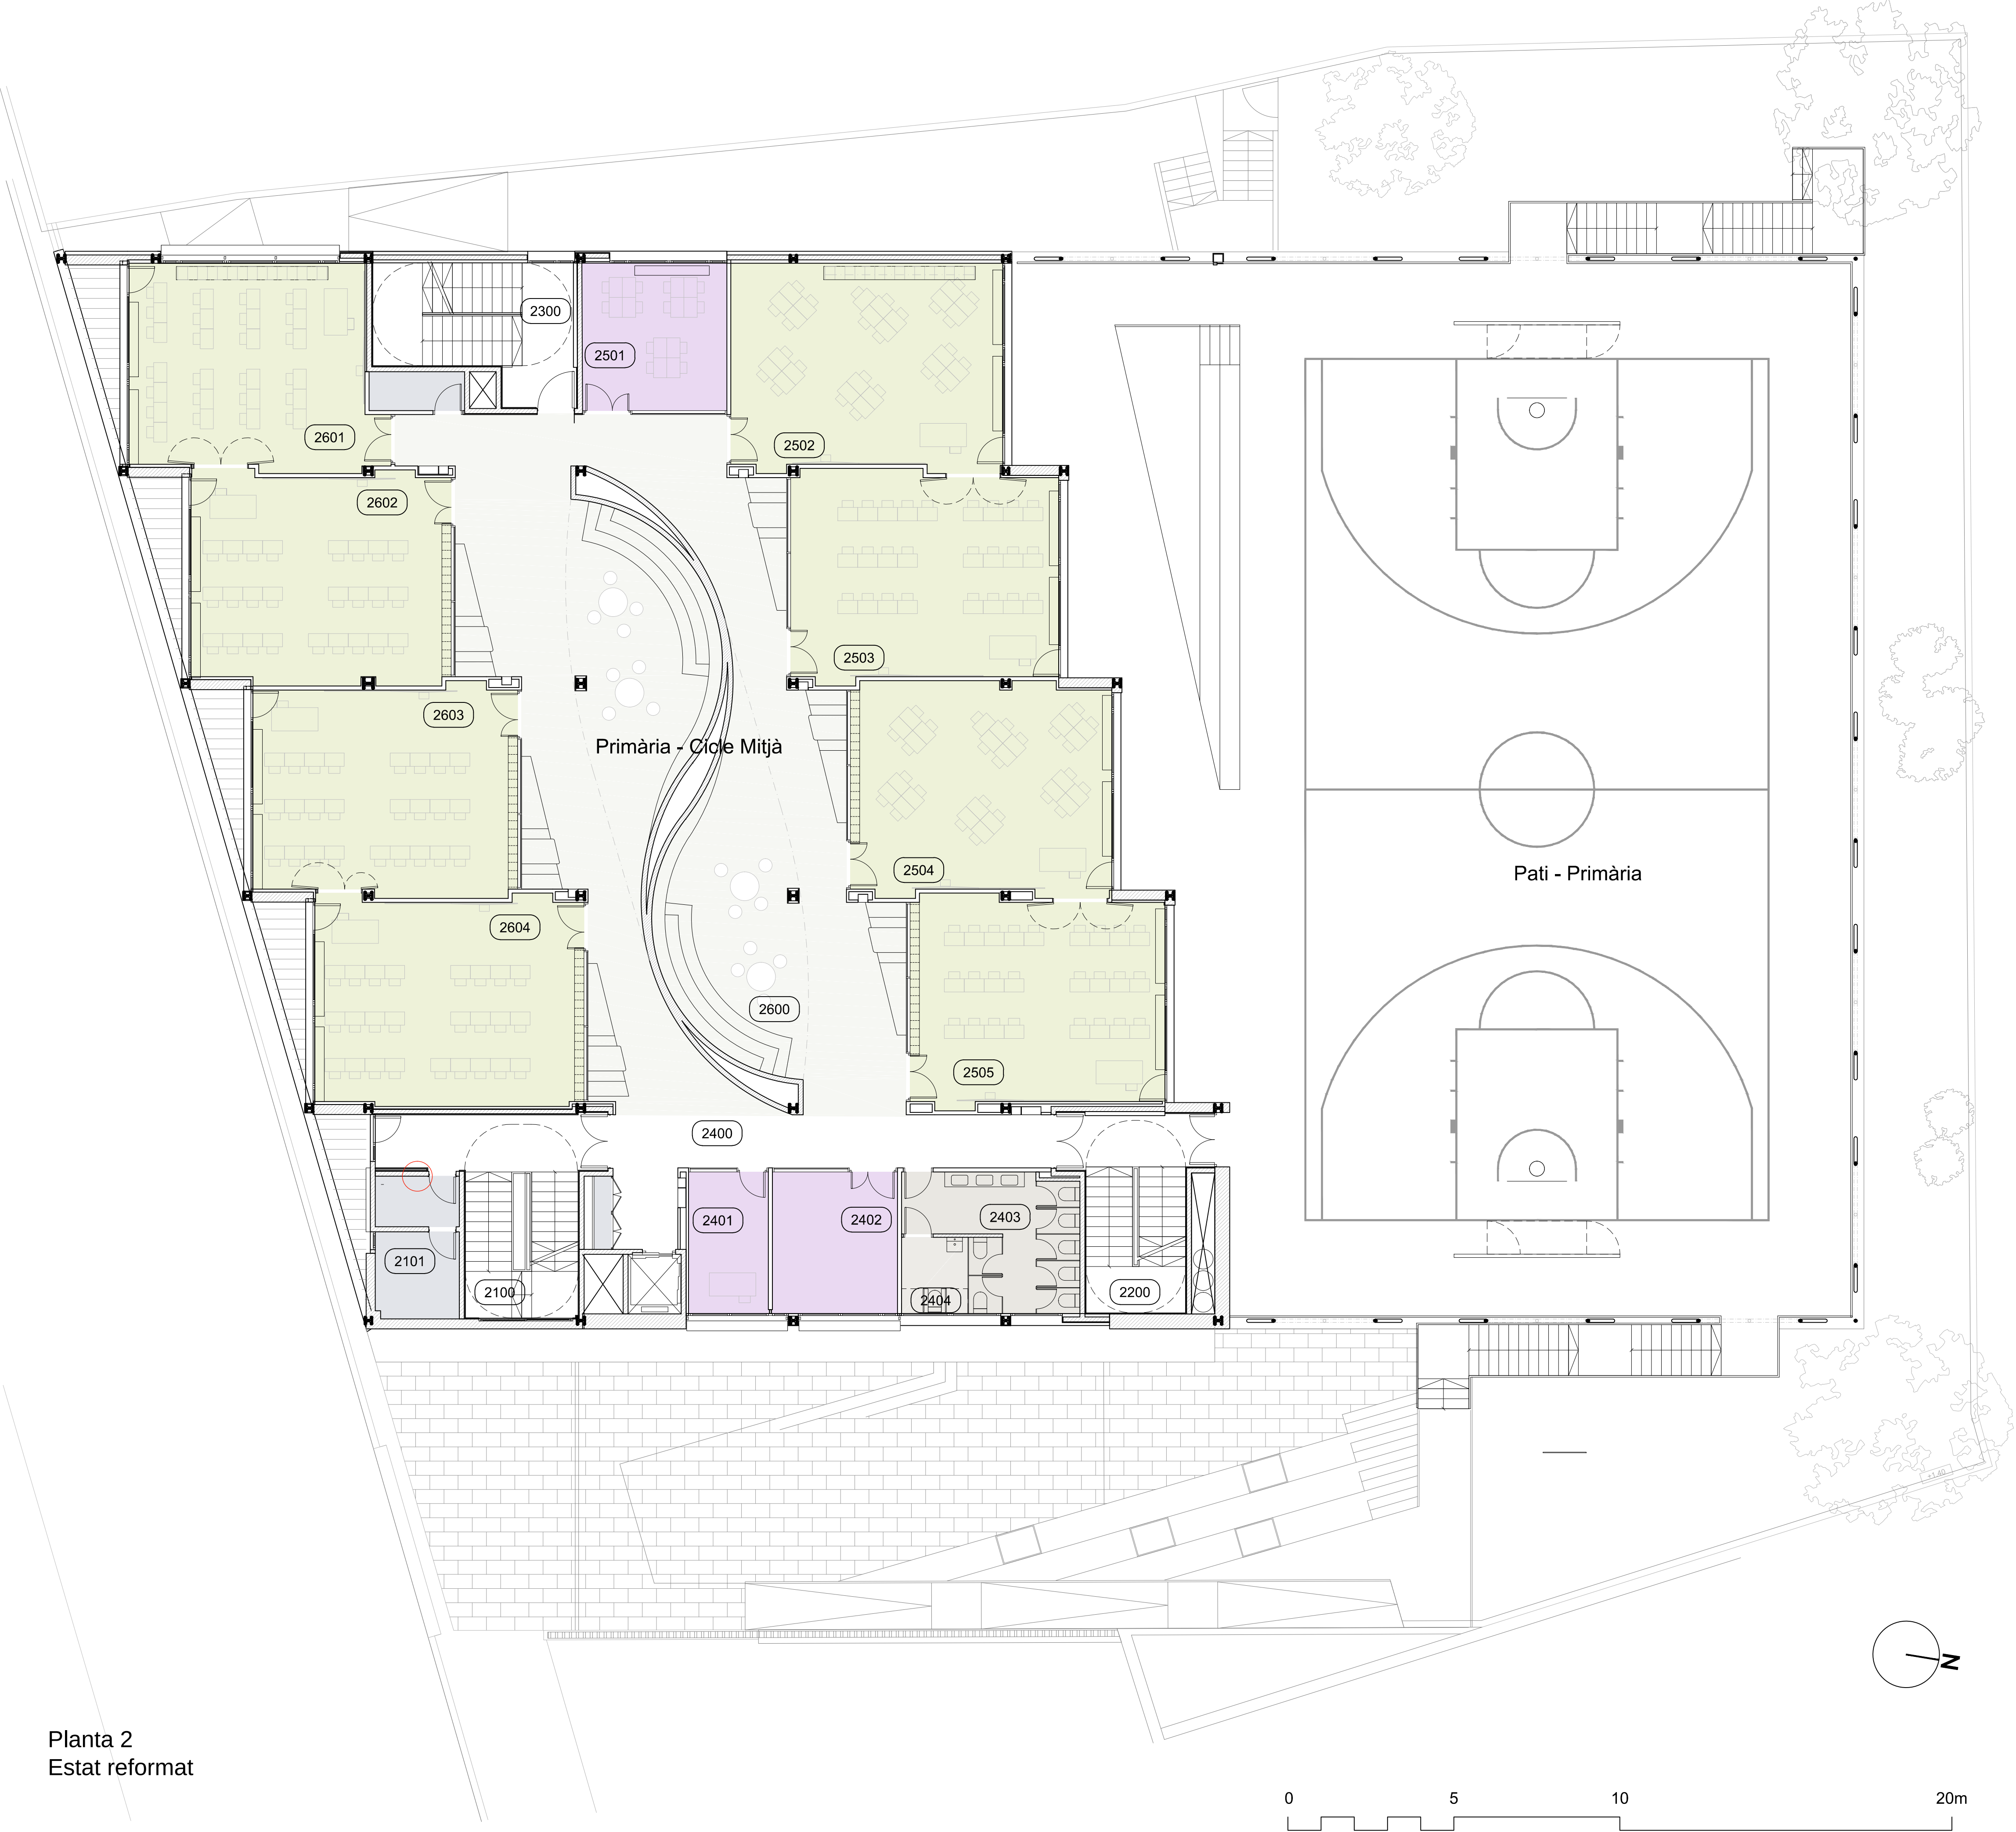



Planta 2
Estat reformat

RESUM ESTAT REFORMAT			
Planta	S.Construïda	Sup Útil	S Exterior
Semi Soterrani	1647.9 m²	1457.2 m²	0.0 m²
Planta Baixa - Planta 1	1604.2 m²	1318.5 m²	876.1 m²
Planta 2	886.4 m²	770.5 m²	757.9 m²
Planta 3	857.2 m²	770.2 m²	0.0 m²
Planta 4	811.3 m²	708.1 m²	96.8 m²
Planta Coberta	34.5 m²	13.2 m²	721.3 m²
TOTAL	5841.5 m²	5037.7 m²	2452.1 m²

SUP ÚTIL PLANTA 2			
Num	Espai		Sup Útil
2100	Escala - A	Circulació	26.6 m²
2101	Espai Tècnic	Espais - Tècnic	6.6 m²
2102	Espai Tècnic	Espais - Tècnic	3.9 m²
2200	Escala - B	Circulació	20.2 m²
2300	Escala - C	Circulació	21.3 m²
2400	Passadis	Circulació	28.3 m²
2401	Aula - Reforç	Primària	10.3 m²
2402	Aula - Reforç	Primària	16.1 m²
2403	Lavabos	Banys - Vestidors	17.6 m²
2404	Lavabo adaptat	Banys - Vestidors	4.6 m²
2405	Armarí elèctric	Espais - Tècnic	1.1 m²
2501	Aula - Auxiliar	Primària	19.4 m²
2502	Aula	Primària - Cicle Superior	50.5 m²
2503	Aula	Primària - Cicle Superior	49.8 m²
2504	Aula	Primària - Cicle Superior	49.8 m²
2505	Aula	Primària - Cicle Superior	47.1 m²
2600	Espai - Comú	Primària - Cicle Mitjà	191.8 m²
2601	Aula	Primària - Cicle Mitjà	45.2 m²
2602	Aula	Primària - Cicle Mitjà	49.3 m²
2603	Aula	Primària - Cicle Mitjà	49.3 m²
2604	Aula	Primària - Cicle Mitjà	50.3 m²
2605	Magatzem	Primària - Cicle Mitjà	3.4 m²
TOTAL			

SUP EXTERIOR PLANTA 2		
Espai		Sup Útil
Terrassa	Terrassa	4.7 m²
Pati - Exterior	Pati - Primària	701.3 m²
Escala - E	Circulació	17.2 m²
Escala - D	Circulació	17.9 m²
Terrassa	Terrassa	5.0 m²
Terrassa	Terrassa	4.9 m²
Terrassa	Terrassa	4.9 m²
Terrassa	Terrassa	4.9 m²
TOTAL		760.8 m²

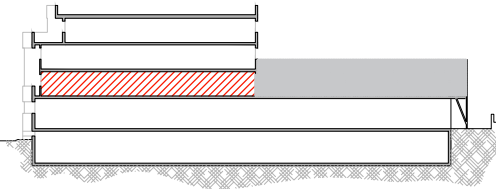


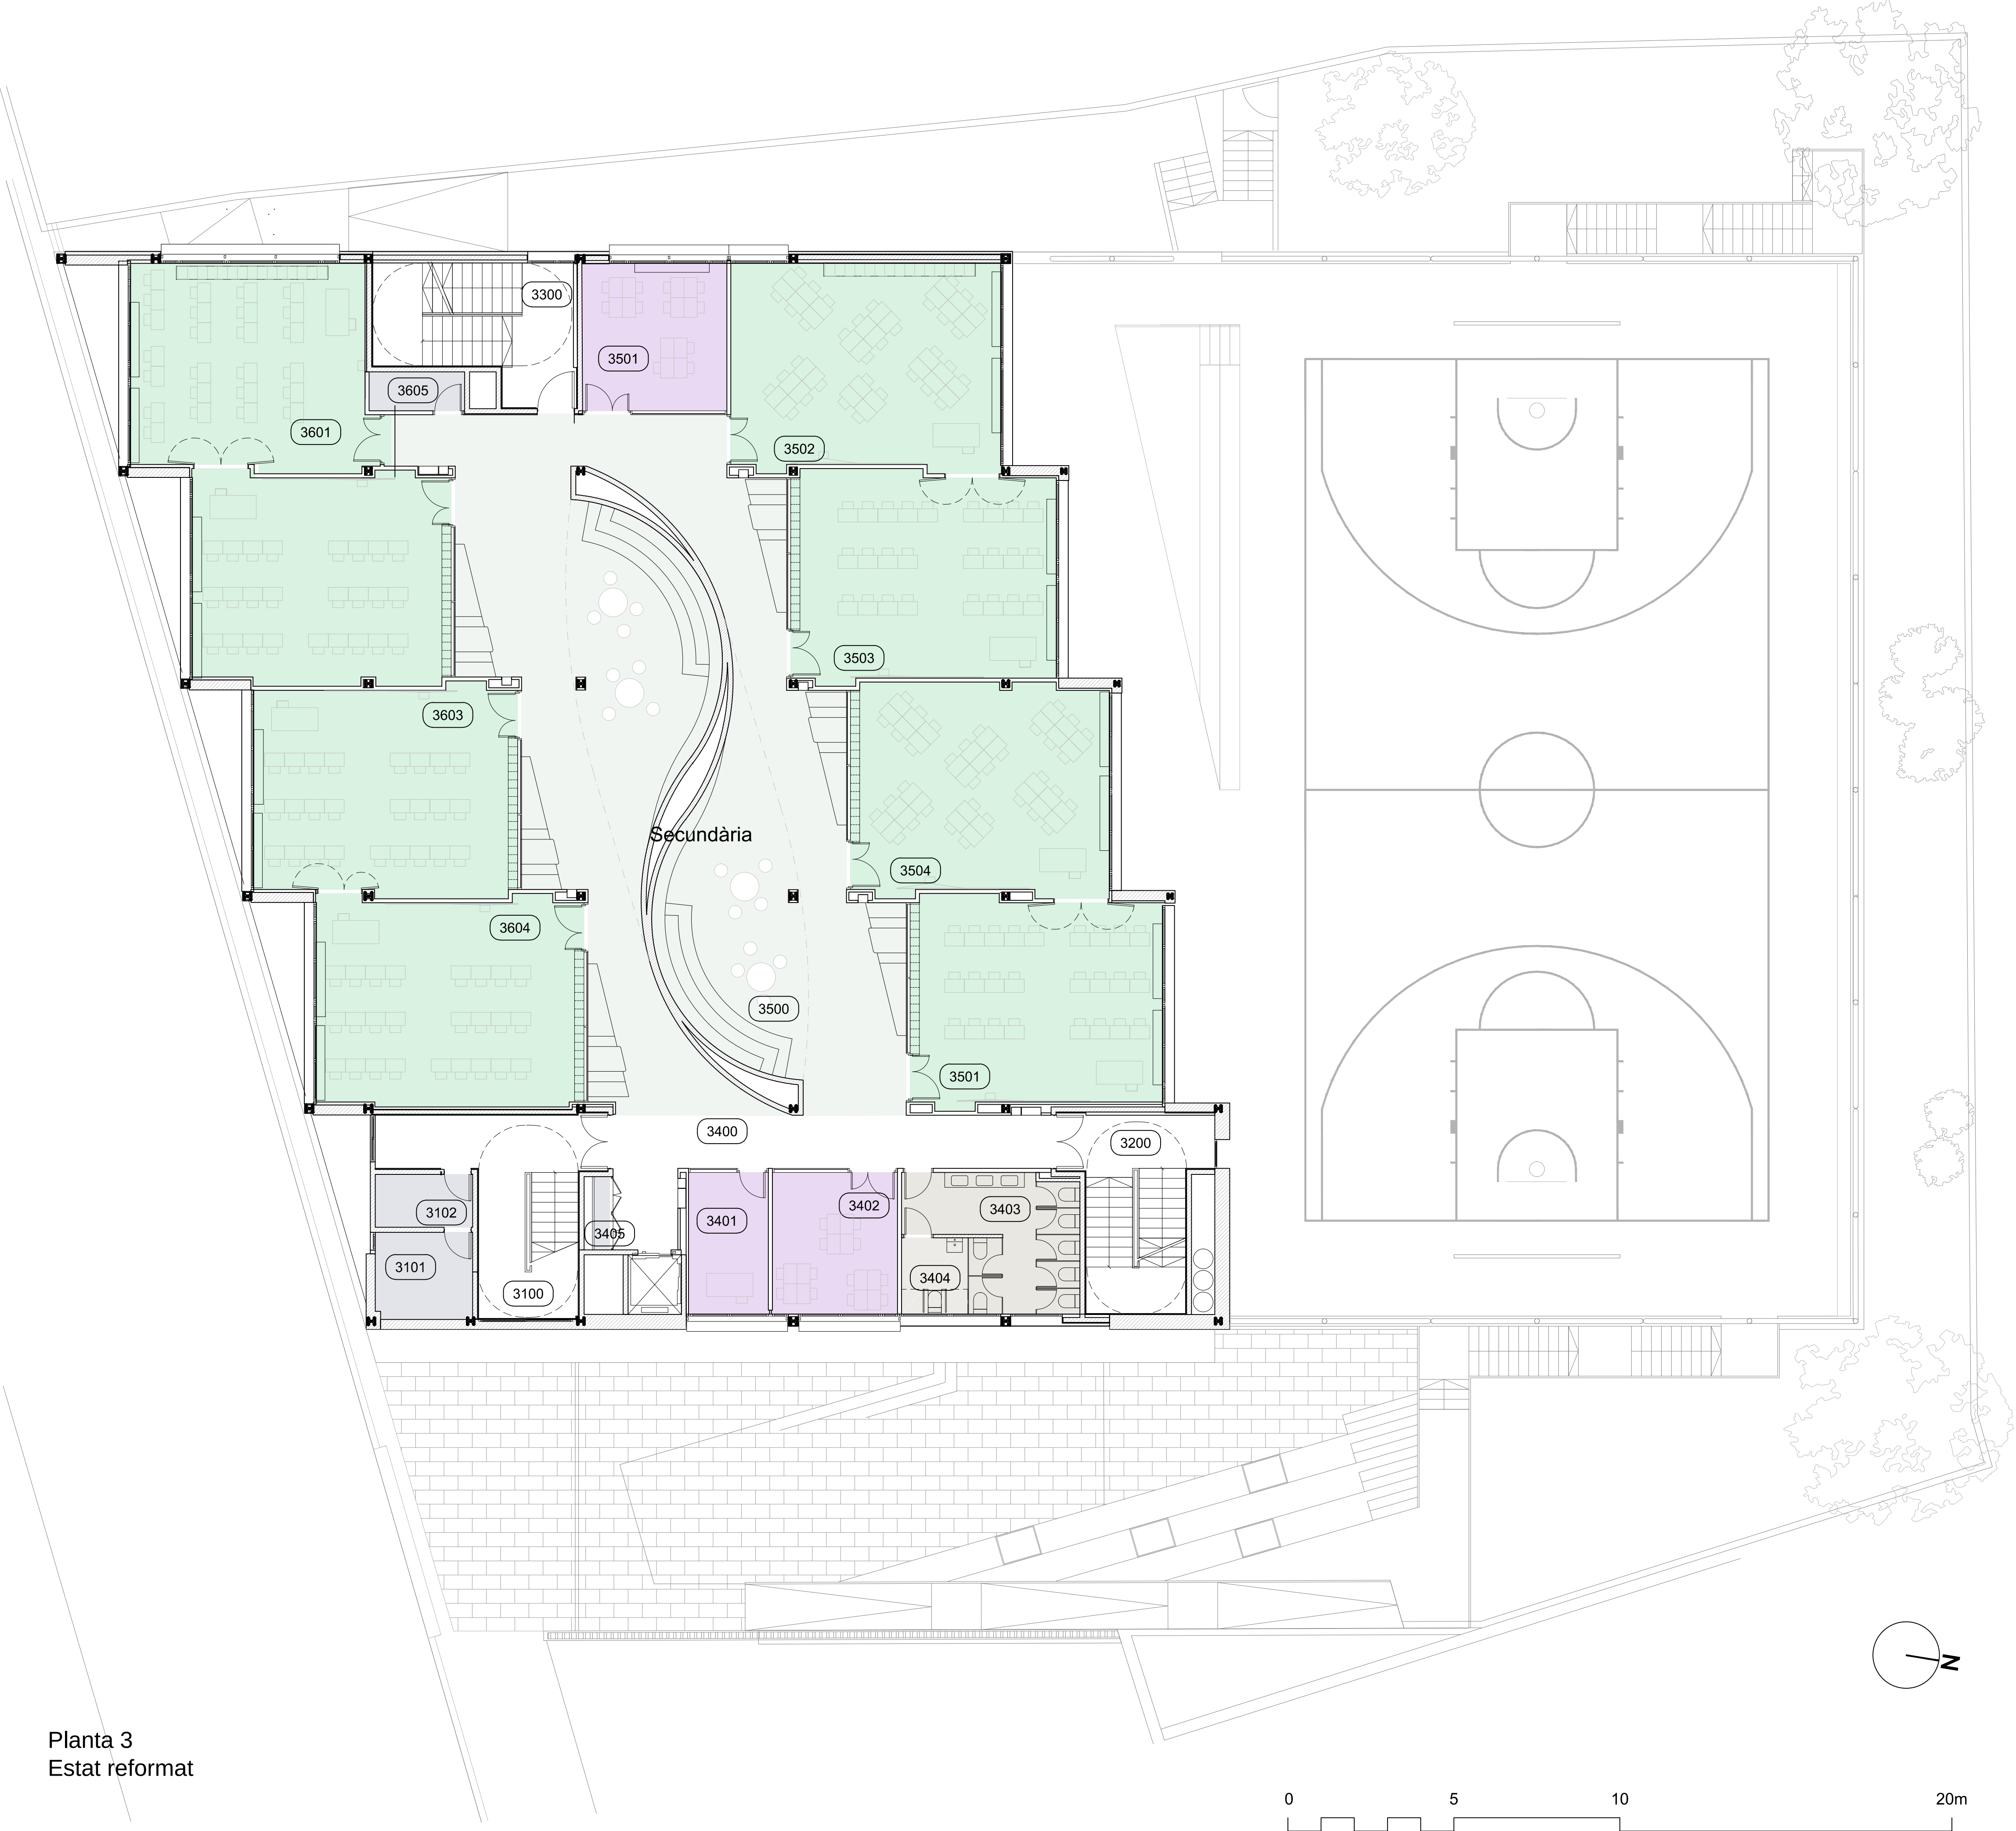


Planta 3
Estat reformat

RESUM ESTAT REFORMAT			
Planta	S.Construïda	Sup Útil	S Exterior
Semi Soterrani	1647.9 m²	1457.2 m²	0.0 m²
Planta Baixa - Planta 1	1604.2 m²	1318.5 m²	876.1 m²
Planta 2	886.4 m²	770.5 m²	757.9 m²
Planta 3	857.2 m²	770.2 m²	0.0 m²
Planta 4	811.3 m²	708.1 m²	96.8 m²
Planta Coberta	34.5 m²	13.2 m²	721.3 m²
TOTAL	5841.5 m²	5037.7 m²	2452.1 m²

SUP ÚTIL PLANTA 3			
Num	Espai		Sup Útil
3100	Escala - A	Circulació	25.0 m²
3101	Espai Tècnic	Espais - Tècnic	7.7 m²
3102	Espai Tècnic	Espais - Tècnic	4.7 m²
3200	Escala - B	Circulació	20.3 m²
3300	Escala - C	Circulació	21.3 m²
3400	Passadis	Circulació	26.1 m²
3401	Despatx	Professors	10.3 m²
3402	Aula - Reforç	Secundària	16.1 m²
3403	Lavabos	Banys - Vestidors	17.6 m²
3404	Lavabo adaptat	Banys - Vestidors	4.6 m²
3405	Armari elèctric	Espais - Tècnic	1.0 m²
3500	Espai - Comú	Secundària	192.3 m²
3501	Aula - Auxiliar	Secundària	19.4 m²
3501	Aula	Secundària	46.6 m²
3502	Aula	Secundària	50.1 m²
3503	Aula	Secundària	49.6 m²
3504	Aula	Secundària	49.2 m²
3601	Aula	Secundària	44.9 m²
3602	Aula	Secundària	49.0 m²
3603	Aula	Secundària	49.2 m²
3604	Aula	Secundària	50.0 m²
3605	Magatzem - Neteja	Manteniment	3.4 m²
TOTAL			

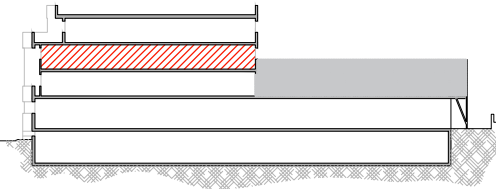

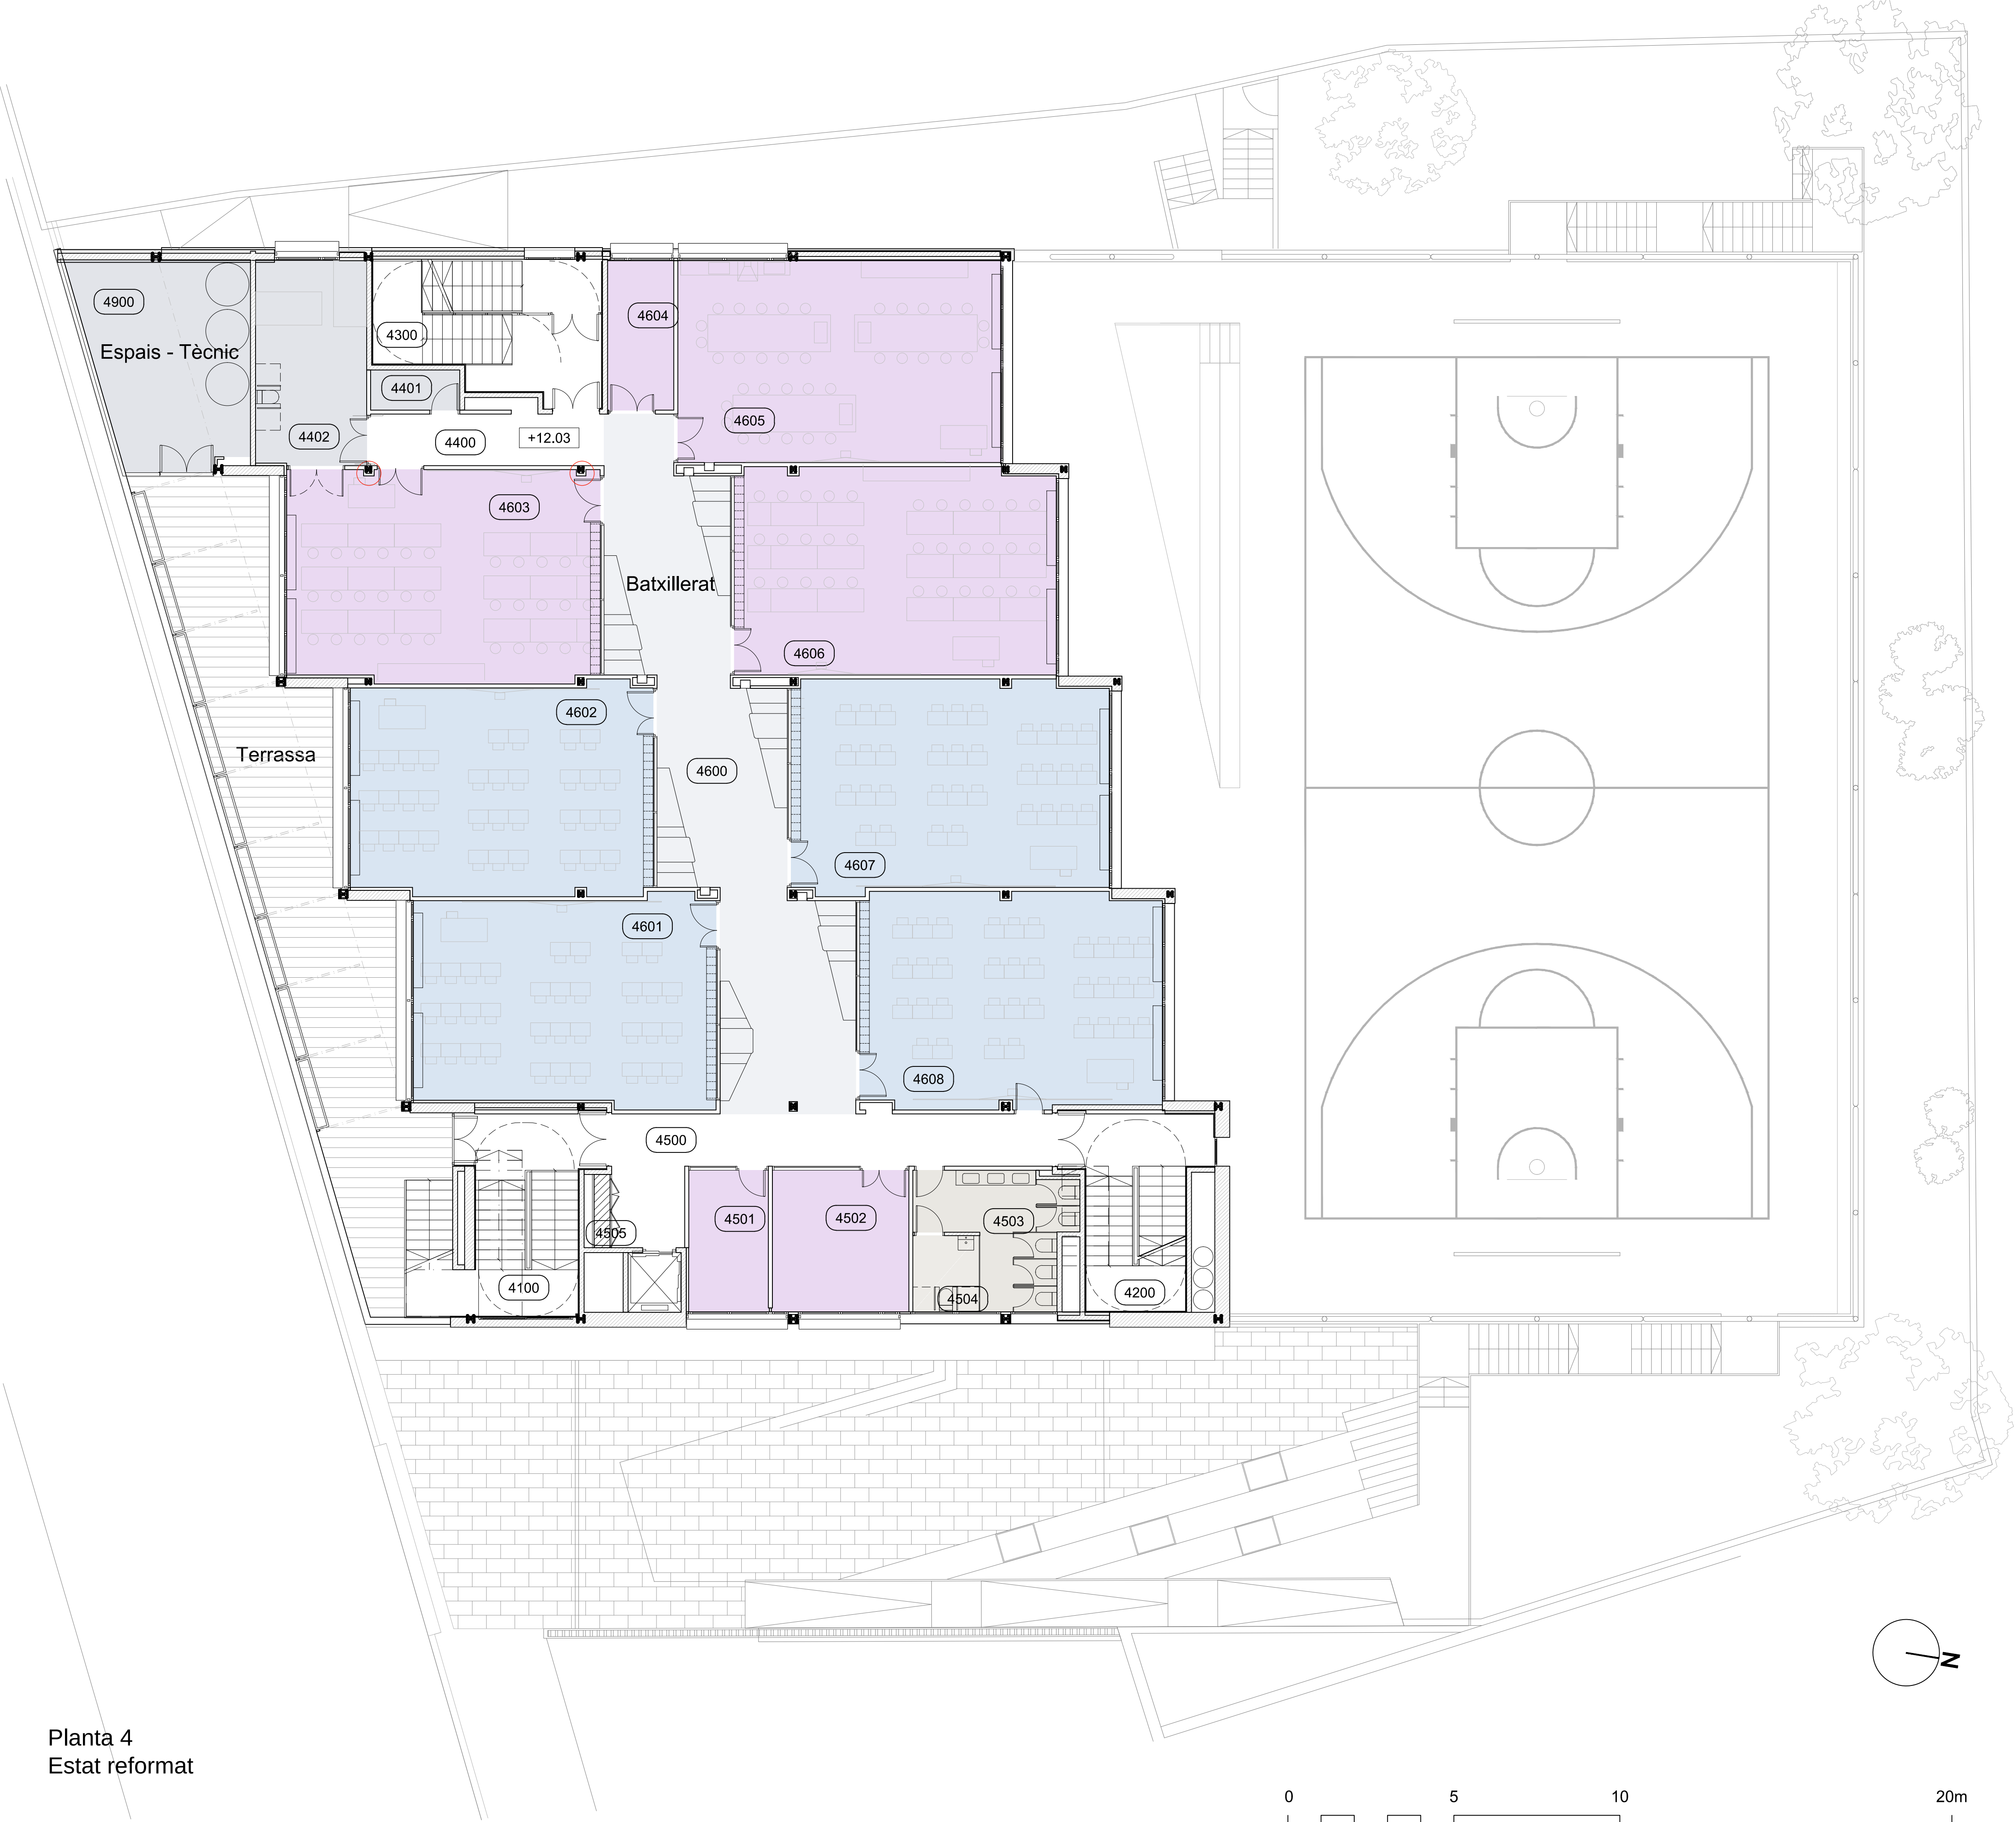


Planta 4
Estat reformat


RESUM ESTAT REFORMAT			
Planta	S.Construïda	Sup Útil	S Exterior
Semi Soterrani	1647.9 m²	1457.2 m²	0.0 m²
Planta Baixa - Planta 1	1604.2 m²	1318.5 m²	876.1 m²
Planta 2	886.4 m²	770.5 m²	757.9 m²
Planta 3	857.2 m²	770.2 m²	0.0 m²
Planta 4	811.3 m²	708.1 m²	96.8 m²
Planta Coberta	34.5 m²	13.2 m²	721.3 m²
TOTAL	5841.5 m²	5037.7 m²	2452.1 m²

SUP ÚTIL PLANTA 4			
Num	Espai		Sup Útil
4100	Escala - A	Circulació	20.7 m²
4200	Escala - B	Circulació	20.1 m²
4300	Escala - C	Circulació	18.0 m²
4400	Passadis	Circulació	10.9 m²
4401	Magatzem - Neteja	Manteniment	3.2 m²
4402	Taller - Formació Professional	Batxillerat	20.6 m²
4500	Passadis	Circulació	26.4 m²
4501	Despatx	Professors	10.2 m²
4502	Aula - Auxiliar	Batxillerat	17.5 m²
4503	Lavabos	Banys - Vestidors	14.6 m²
4504	Lavabo adaptat	Banys - Vestidors	4.6 m²
4505	Armari elèctric	Espais - Tècnic	1.1 m²
4600	Espai - Comú	Batxillerat	78.2 m²
4601	Aula	Batxillerat	56.1 m²
4602	Aula	Batxillerat	57.0 m²
4603	Laboratori - Ciències	Batxillerat	60.0 m²
4604	Aula - Reforç	Batxillerat	9.0 m²
4605	Laboratori - Ciències	Batxillerat	59.3 m²
4606	Laboratori - Ciències	Batxillerat	60.2 m²
4607	Aula	Batxillerat	60.0 m²
4608	Aula	Batxillerat	58.5 m²
4900	Espai Tècnic	Espais - Tècnic	29.5 m²

TOTAL

SUP EXTERIOR PLANTA 4			Sup Útil
Espai			85.3 m²
Terrassa	Terrassa		7.1 m²
Escala - C	Circulació		5.5 m²
Escala - A	Circulació		
0			97.8 m²

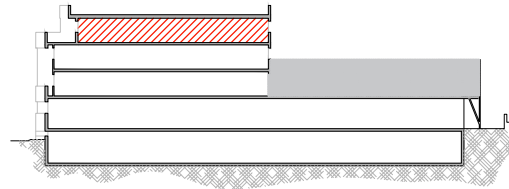

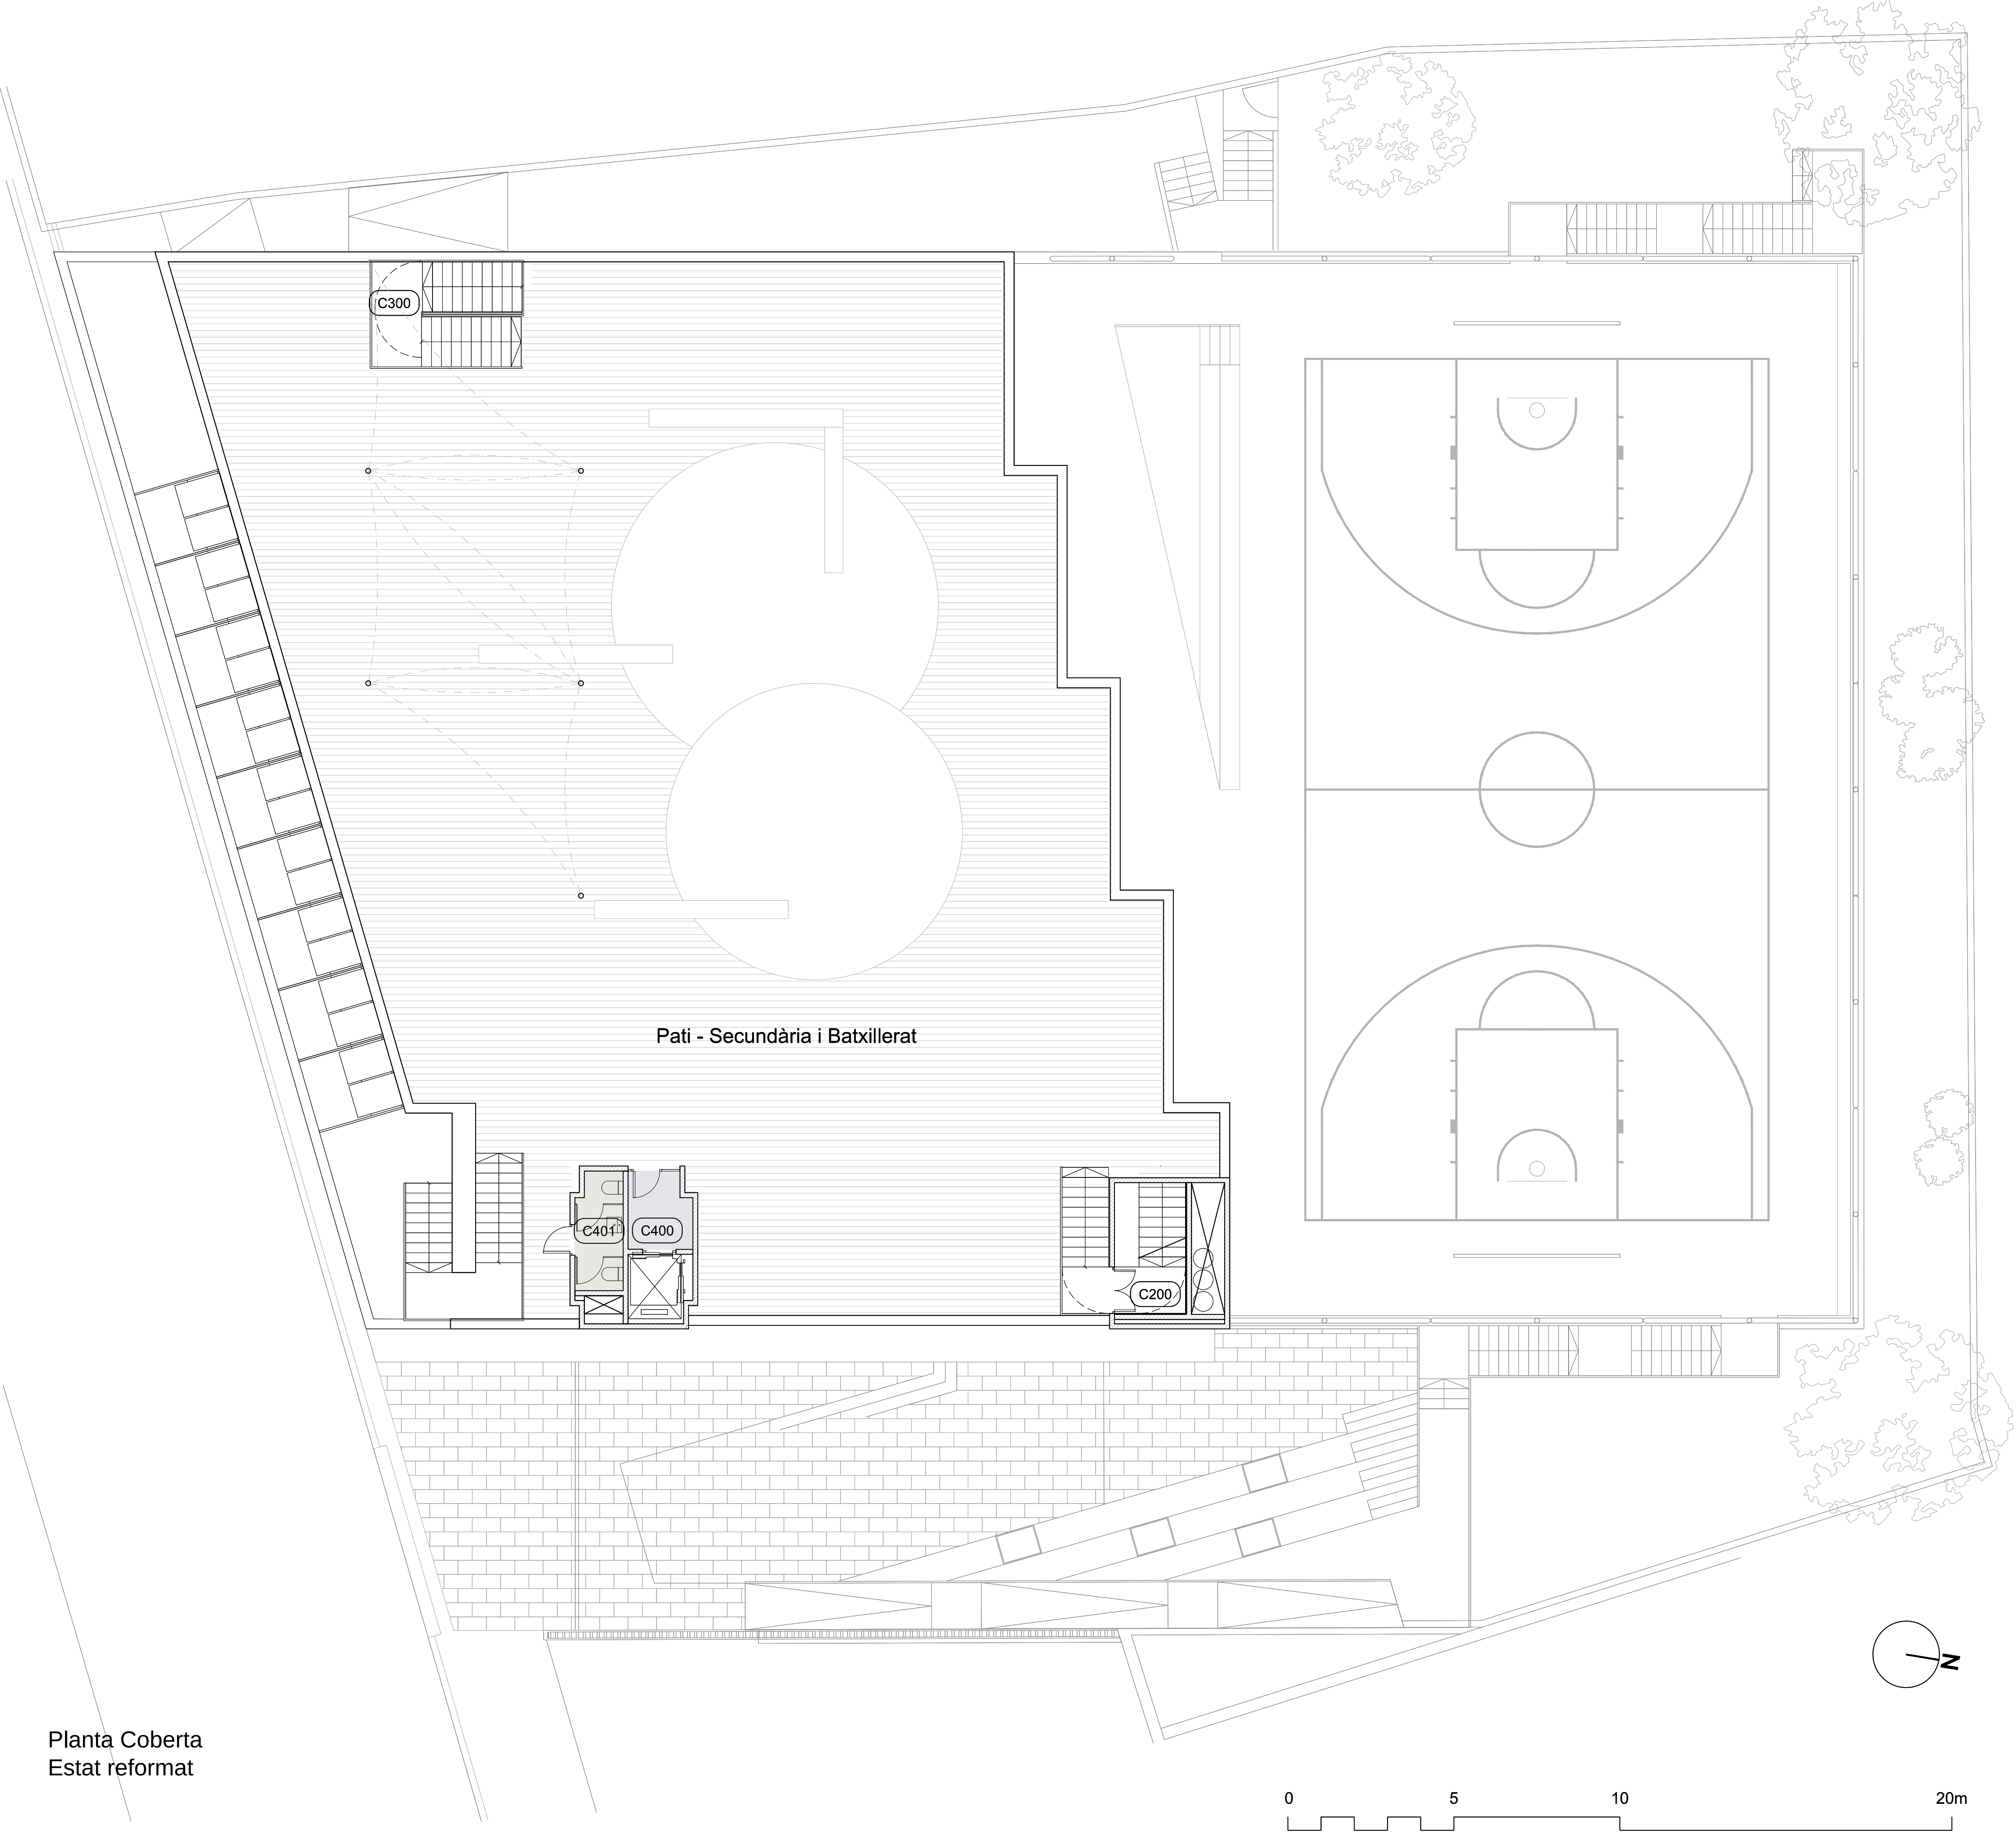



Planta Coberta
Estat reformat

RESUM ESTAT REFORMAT			
Planta	S.Construïda	Sup Útil	S Exterior
Semi Soterrani	1647.9 m²	1457.2 m²	0.0 m²
Planta Baixa - Planta 1	1604.2 m²	1318.5 m²	876.1 m²
Planta 2	886.4 m²	770.5 m²	757.9 m²
Planta 3	857.2 m²	770.2 m²	0.0 m²
Planta 4	811.3 m²	708.1 m²	96.8 m²
Planta Coberta	34.5 m²	13.2 m²	721.3 m²
TOTAL	5841.5 m²	5037.7 m²	2452.1 m²

SUP ÚTIL PLANTA COBERTA			
Num	Espai		Sup Útil
C200	Escala - B	Circulació	3.9 m²
C400	Vestíbul	Circulació	4.3 m²
C401	Lavabos	Banys - Vestidors	5.0 m²
0			

SUP EXTERIOR PLANTA COBERTA			
Espai			Sup Útil
Escala - A	Circulació		8.1 m²
Escala - B	Circulació		6.3 m²
Escala - C	Circulació		10.2 m²
Pati - Exterior	Pati - Secundària i Batxillerat		689.1 m²
TOTAL			713.7 m²

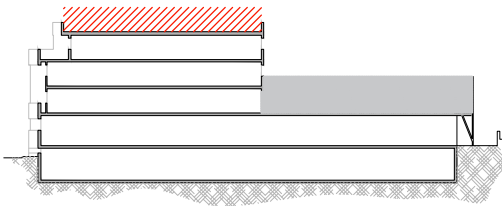

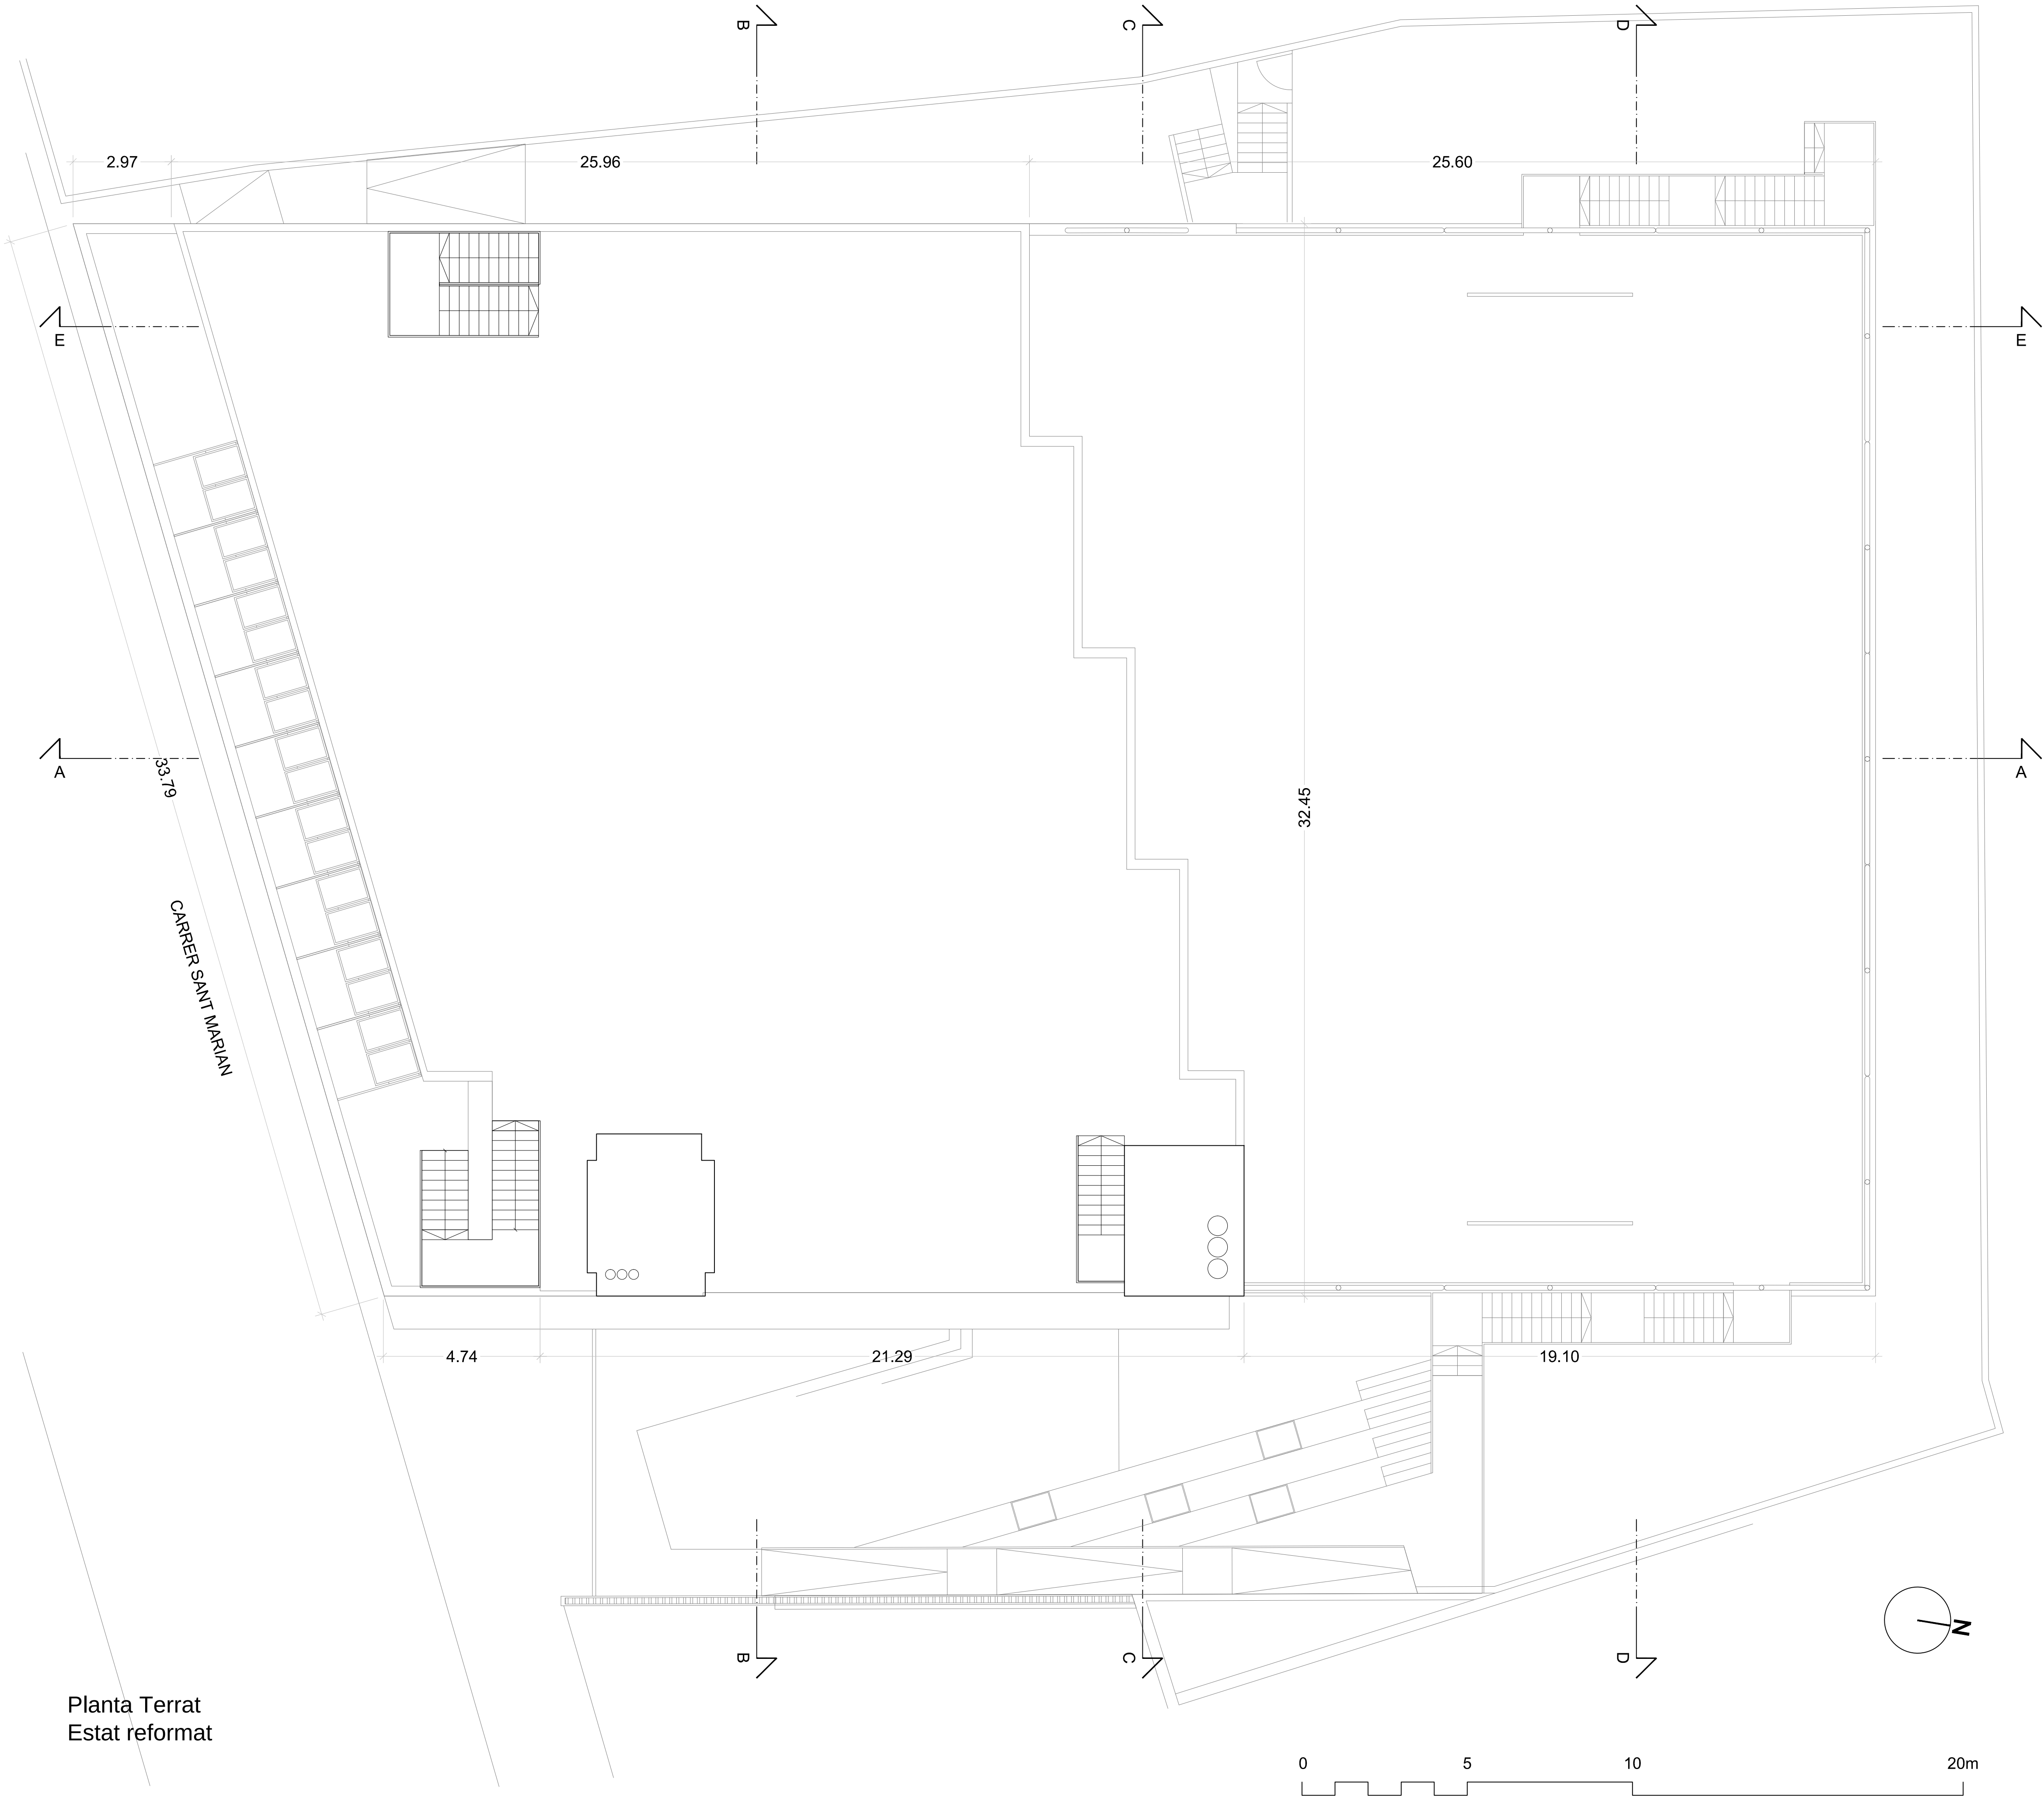

Planta Terrat
Estat reformat

RESUM ESTAT REFORMAT			
Planta	S.Construïda	Sup Útil	S Exterior
Semi Soterrani	1647.9 m²	1457.2 m²	0.0 m²
Planta Baixa - Planta 1	1604.2 m²	1318.5 m²	876.1 m²
Planta 2	886.4 m²	770.5 m²	757.9 m²
Planta 3	857.2 m²	770.2 m²	0.0 m²
Planta 4	811.3 m²	708.1 m²	96.8 m²
Planta Coberta	34.5 m²	13.2 m²	721.3 m²
TOTAL	5841.5 m²	5037.7 m²	2452.1 m²

