





Situació
Escala DIN A1 = 1:2000, DIN A3 = 1:4000

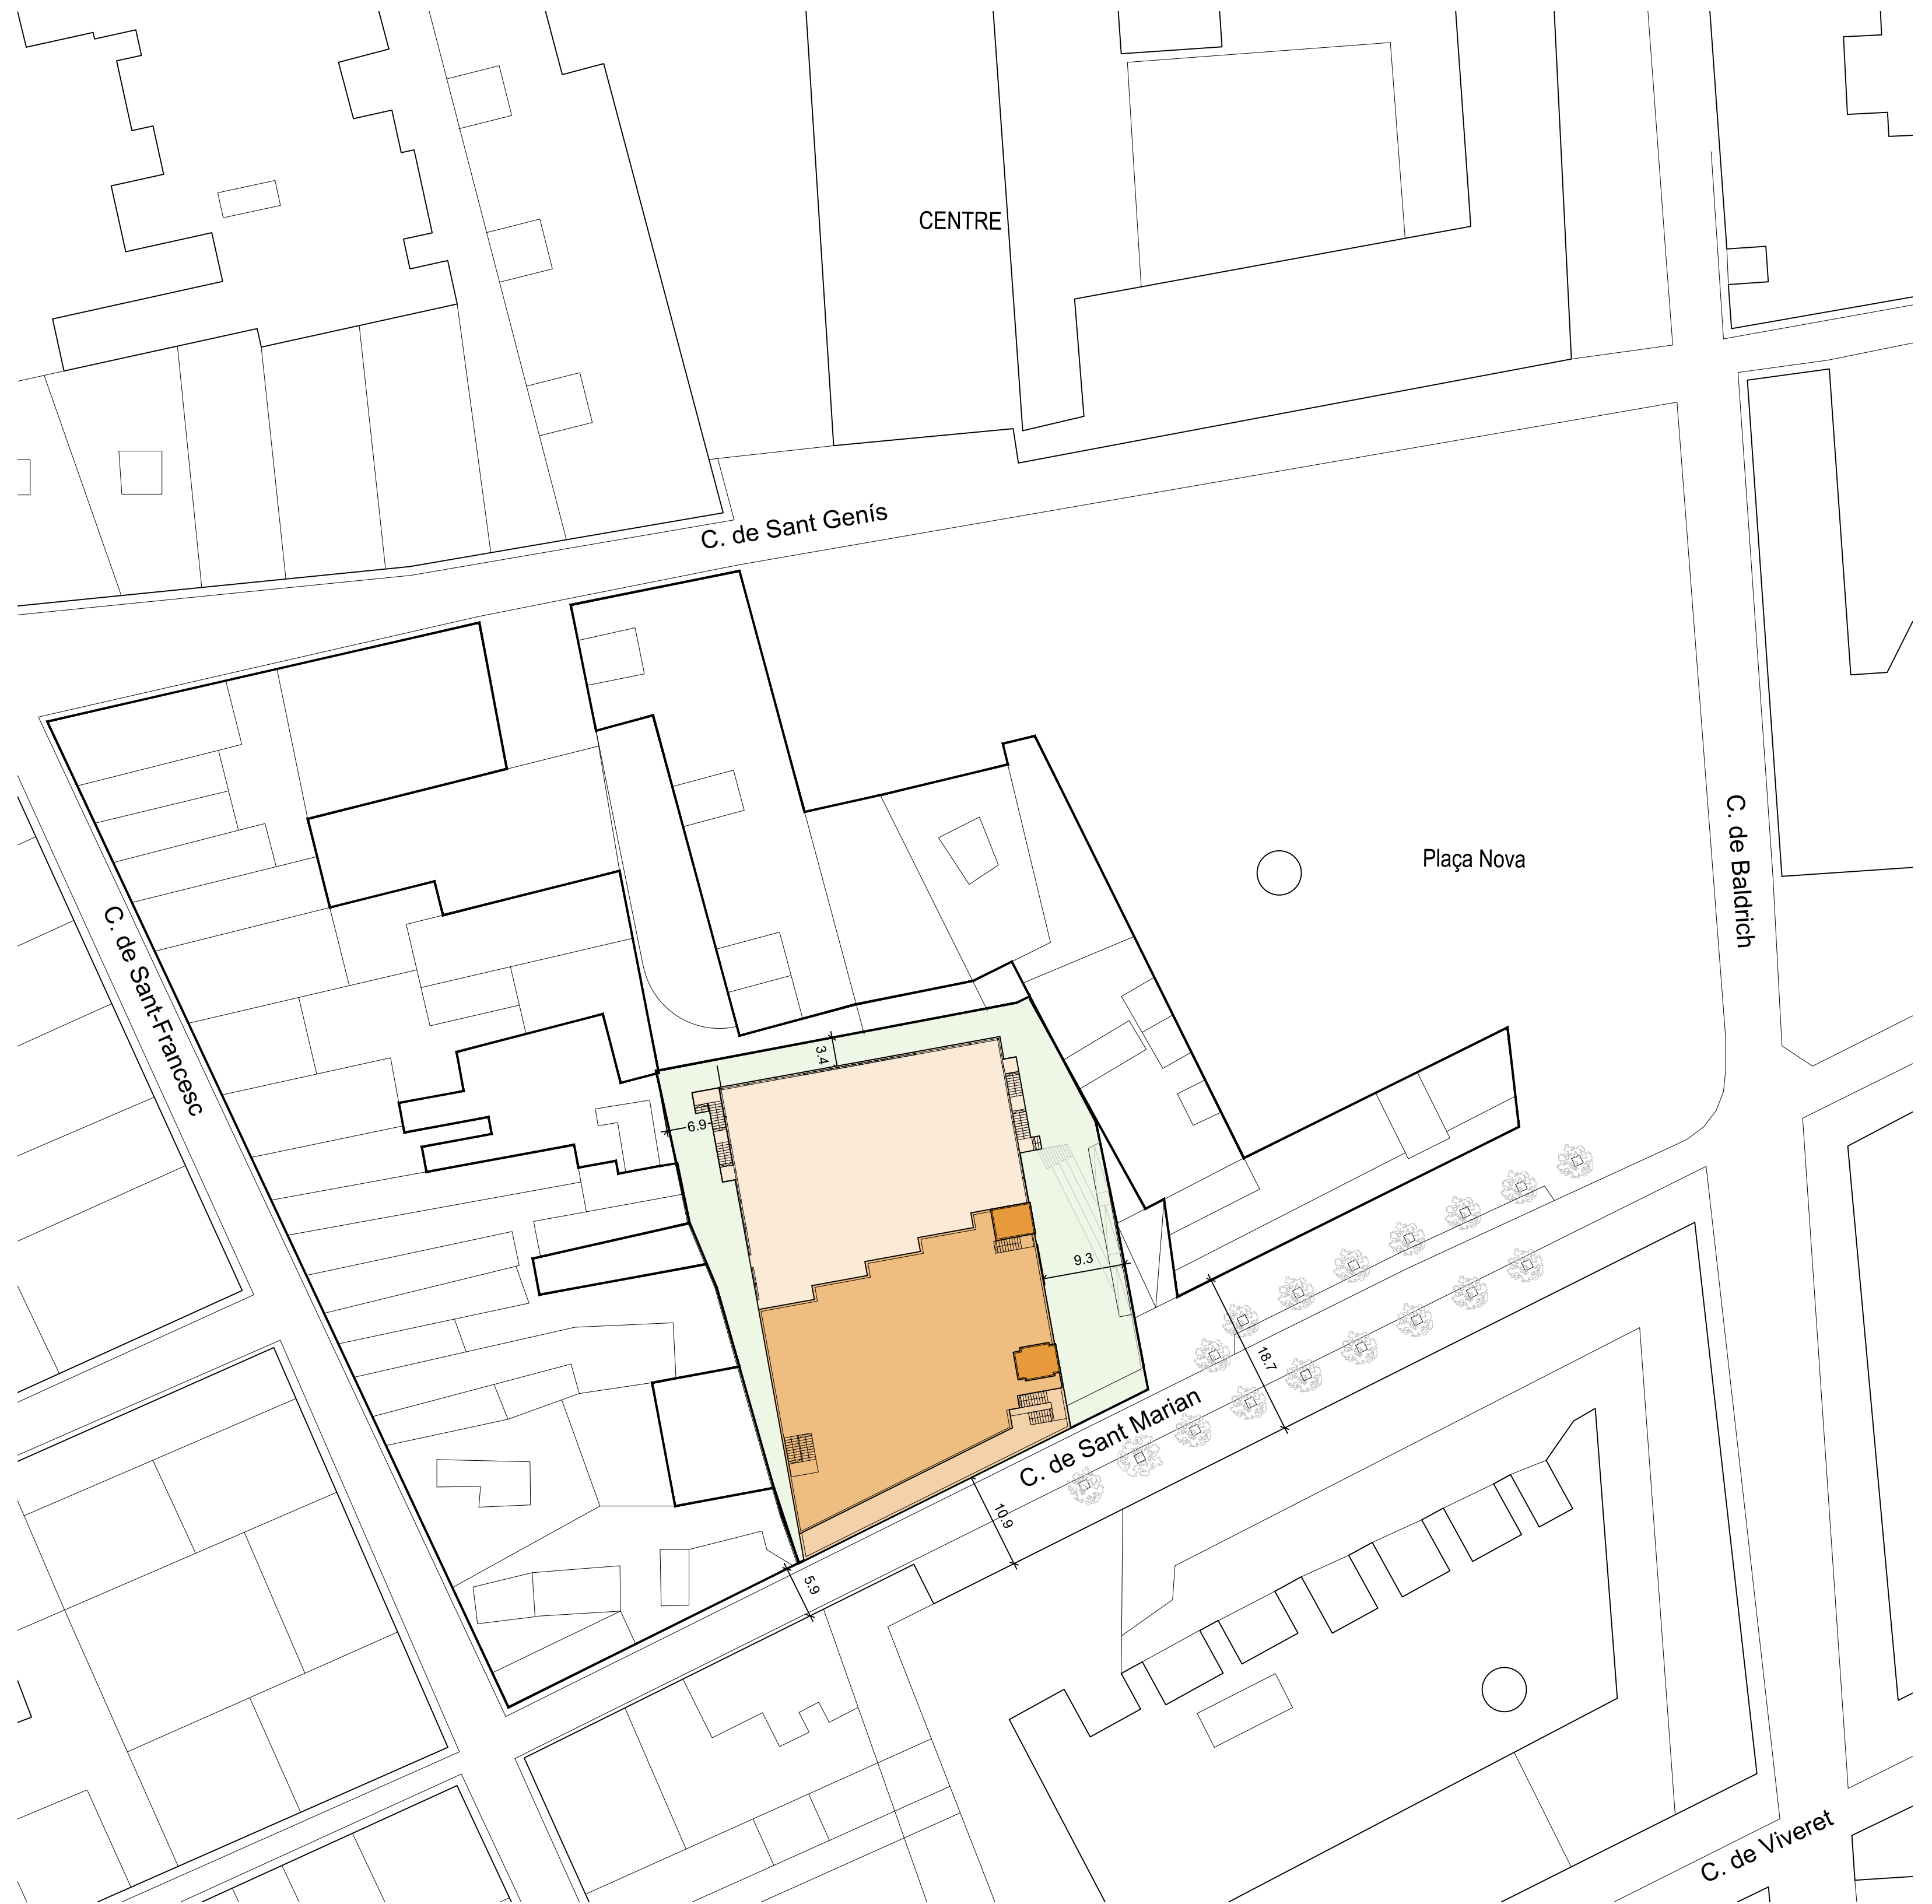

Emplaçament
Escala DIN A1 = 1:500, DIN A3 = 1:1000

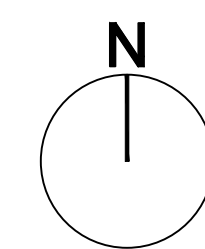

c/ Sant Marian 98-100, Terrassa

Zona urbana. Clau A8.0 "industrial en illa tancada"
Tipus ordenació: alineació a vial
Superfície parcel·la: 2.303 m²

PT
PC
P4
P3
P2
P1
PB
PSS



Façana Oest

PT
PC
P4
P3
P2
P1
PB
PSS



Façana Sud a carrer Sant Marian

